从平面依据到可编辑立面

四间卧室分别设置A/B/C/D向立面；每个立面独立图幅。
原生尺寸、填充、带属性图块与锁定视口保留于DWG；模型和节点按毫米1:1绘制。

图号	内容
GE-00—02	目录、尺寸状态、材料与原平面索引
EL-01—04	主卧四向立面
EL-05—08	次卧四向立面
EL-09—12	女儿房四向立面
EL-13—16	男孩房四向立面
JB-01—03	衣柜内部、剖面、薄柜与玩具柜深化
ND-01—05	D01—D09柜体、饰面、门窗与灯槽节点

尺寸状态与适用边界

P = 原平面尺寸或可回溯几何。
I = 效果图可见的设计意向。
D = 新增设计建议，可复核和调整。
U = 缺少可靠依据，保持待确认。
竖向未确认段采用省略或折断表达；不以其他项目层高替代本项目H。
门扇几何宽不等于门洞净宽；柜门定位模数不等于净空或下料宽。
尺寸是原生DIMENSION并生成显示块；并非与任意手工修改的轮廓完全关联。

本版实质修订

主卧东向书桌侧投影由距北端600修正为50，深550，源对象9156。
女儿房窗边原家具轮廓2380保留，按P63补为桌1400+座980[D]；取消无源1650桌宽。
女孩房B向取消将前景床头柜误画为三门高柜；男孩房玩具柜回到矮柜意向。
新增衣柜门缝/板厚/净格分别计算、底顶构造、软饰面基层及窗台协调节点。

待完成：四间完成净高、门窗竖向复测、材料样板与厂家连接审核。
本版为深化审阅稿；不能作为未经复尺及签审的施工或下料文件。

灰底用于表示后退面/柜内背板，非材料实际色号；前景遮挡线与材料色号分别核对。

材料编码 / 做法及参数表

同一编码对应一种材料类别；厚度及安装建议均以D标明

编码	效果意向	基层 / 面层 / 收口	依据与状态
M01	暖白/浅米墙面	墙面找平/底涂/面涂；基层及品牌待核	P45/54/60/65；I，做法D
M02	自然木色木作	柜身18、门板18、封边及五金按柜厂；D	平面轮廓P，面层I/D
M03	织物/软饰面	软饰层10+基层12[D]；样板及防火等级待确认	P47/54—56；I，构造D
M04	粉/绿织物感斜顶面	织物感来自效果；具体材质样板及成品厂家深化	P60—63/65—67；I
M05	保留原窗/纹理内窗	原窗框扇及开启复测；套板12[D]，密封边3[D]	窗宽P；窗高部分P/其余U
M06	木地板及踢脚	选材、地面完成厚待核；踢脚高60[D]	效果意向I，做法D
M07	吊顶/窗帘盒/灯槽	顶板、龙骨及吊挂专项确认；槽净宽180[D]	意向I，净高及梁底U
M08	蓝色哑光装饰面	饰面板/涂装选型待定；圆饰不作结构开洞	P67可见意向I，位置D
M09	暖灰哑光柜门面	与M02木色柜身分材质；饰面板/涂装待选型	P60可见哑光意向；D
M10	黑色金属感五金	原窗框保留；新增把手及灯具按产品选型	效果可见I；规格U

统一D参数（不是已确认实测）

柜高2400；柜身/门板18；门缝3；踢脚80；桌高750、板厚25；窗边座高500。


软饰面10+基层12；木收边3分缝；窗帘槽180净宽×150建议预留深度；灯带选型后复核槽口。

节点示意固定件仅表达连接位置；锚固规格、间距、承载及防火条件由设计/厂家结合基层复核。


儿童房600窗台与750桌面相差150；未取得开扇及现场数据前，该冲突不视为解决。

原平面索引 / 展开方向与几何依据

矢量轮廓摘取自上传DXF；仅用于建立平面投影关系

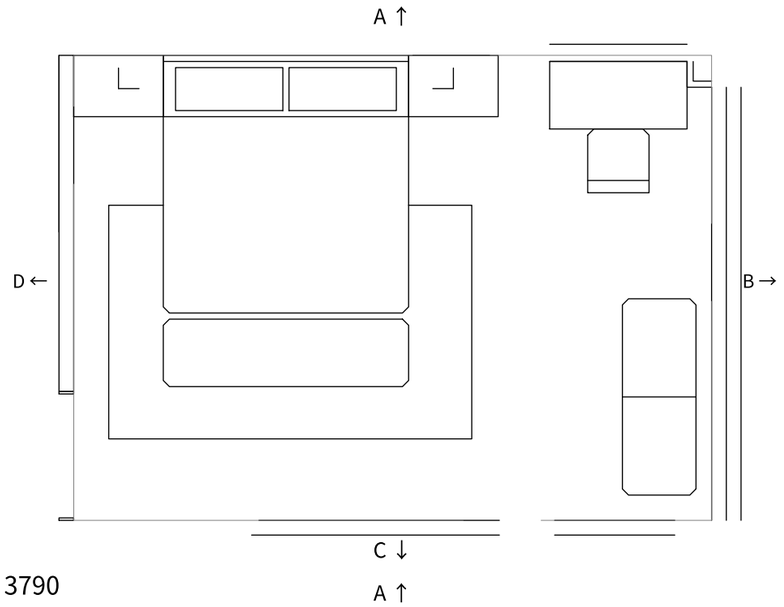

主卧 / 5200 × 3790

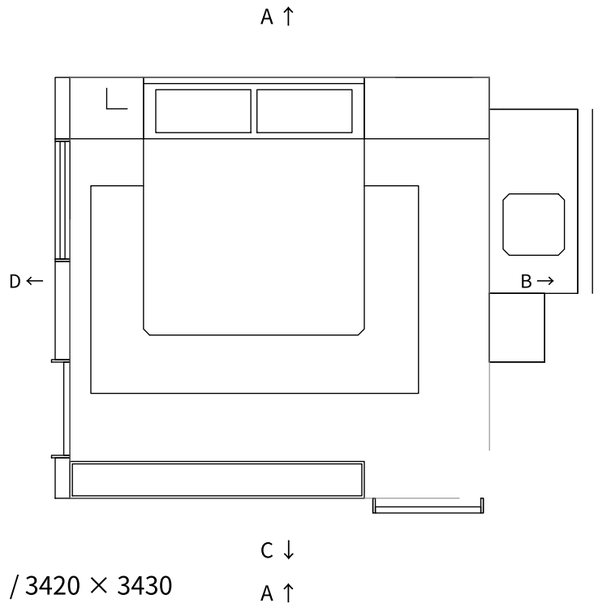

次卧（效果图称老人房） / 3420 × 3430

女儿房 / 5450 × 3010

男孩房 / 5450 × 2870

男孩房2870为柜后墙基准，柜前2670及2690尺寸链端点不同。衣帽间独立区域不在卧室四向范围内。
索引布局保留主要边界和家具投影；源对象与尺寸记录随包附JSON，原上传文件保持只读。

西湖豪庭 2#2单元603	卧室深化 / R04	GE-02	1:50	待签审

主卧 / A 向立面

朝原平面上侧 · 平面范围P；构造及新增高度D；未知总高H不补成实测值

M01 墙面涂装


找平及面涂；基层U

M03 织物感软饰

面层及基层详D04

M02 木色桌板

木种、纹路以样板为准

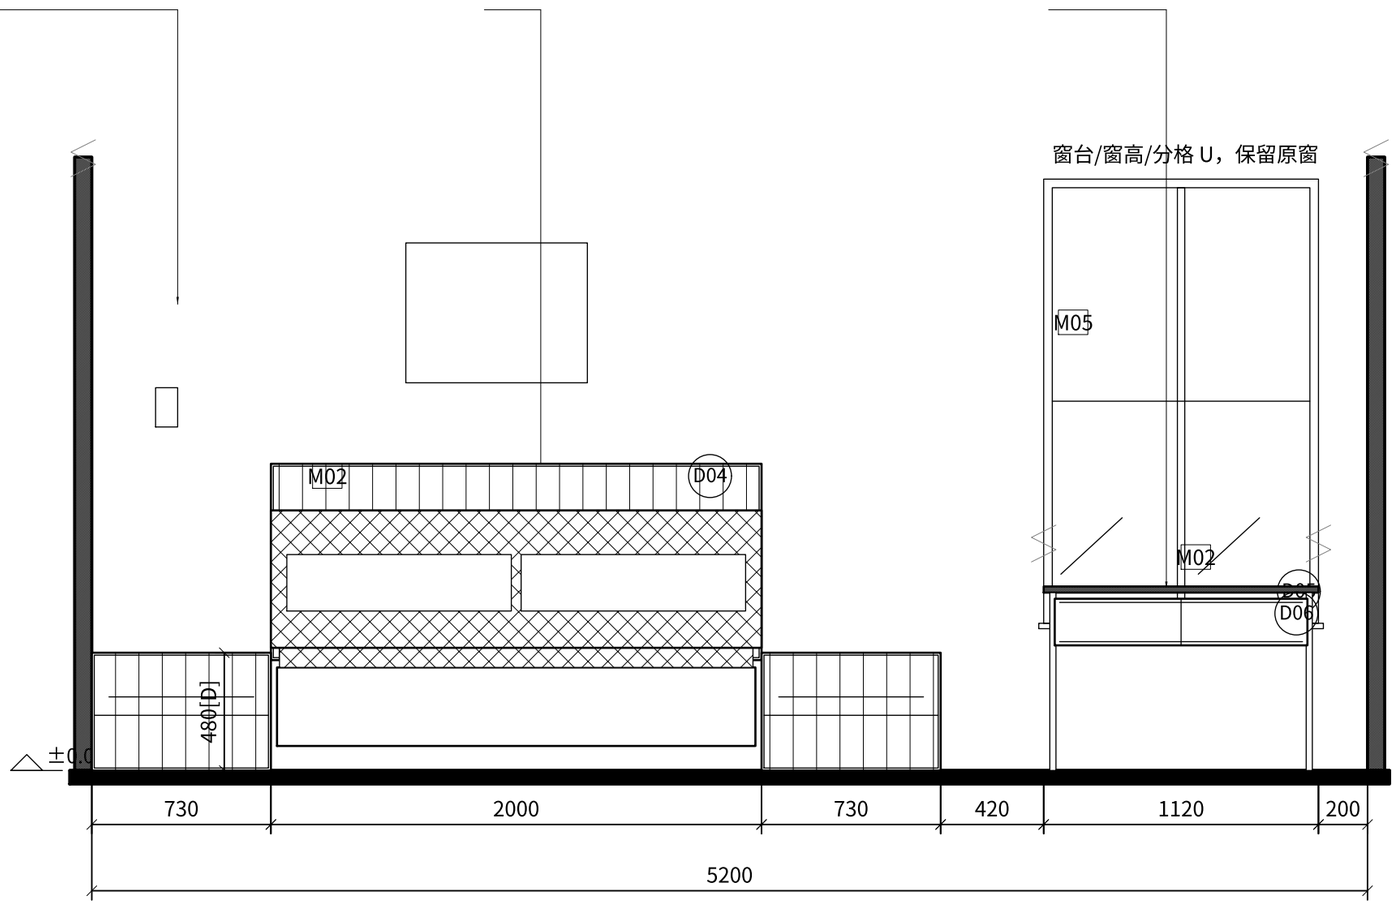

主图尺寸：P为原图，D为设计建议；门窗竖向未确认项见右栏

01 / 材料及做法

M01 墙面涂装
M02 木作饰面
M03 织物/软饰面
M06 地板及踢脚
编码对应GE-01材料表。

02 / 节点索引

D04 床头饰面与边框
D06 桌板及窗台协调

03 / 原图与效果依据

P45–50效果意向。
原DXF几何见GE-02。


04 / 待协调事项

吊顶完成净高H、材料样板及固定条件待确认。

P 原图	平面5200×3790；深3790由墙线几何读取。
I 意向	P45–50；图面未覆盖部位列为建议，不冒称效果图已有。
D 深化	床头木作上口1250、床头柜480、壁灯中1480为D。
U 待核	吊顶净高、门窗竖向、饰面选型及连接条件，详GE-00。

主卧 / B 向立面

朝原平面右侧 · 平面范围P；构造及新增高度D；未知总高H不补成实测值

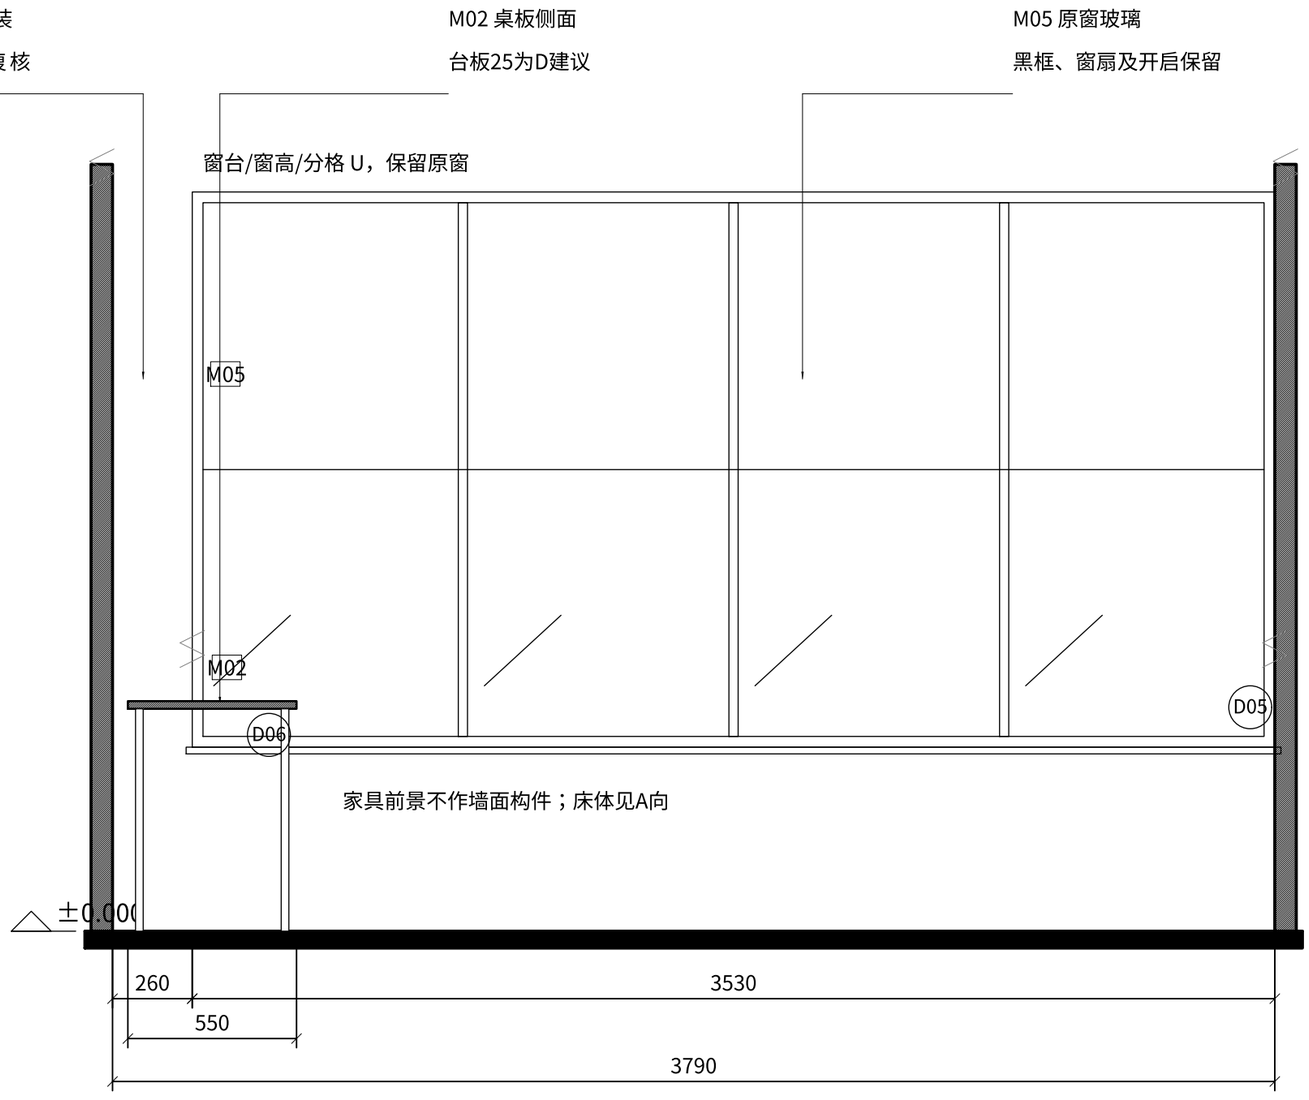

01 / 材料及做法

M01 墙面涂装
M02 木作饰面
M03 织物/软饰面
M06 地板及踢脚
编码对应GE-01材料表。

02 / 节点索引

D05 原窗窗套平剖
D07 窗帘盒与吊顶

03 / 原图与效果依据

P45–50效果意向。
原DXF几何见GE-02。

04 / 待协调事项

吊顶完成净高H、材料样板及固定条件待确认。

P 原图	平面5200×3790；深3790由墙线几何读取。
I 意向	P45–50；图面未覆盖部位列为建议，不冒称效果图已有。
D 深化	书桌侧投影修正为距北端50、深550；原窗分格U。
U 待核	吊顶净高、门窗竖向、饰面选型及连接条件，详GE-00。

主卧 / C 向立面

朝原平面下侧 · 平面范围P；构造及新增高度D；未知总高H不补成实测值

M05 原窗玻璃


套板及密封边详D05

M01 墙面涂装

效果图未覆盖区为D

M06 木地板

完成厚度及色样U

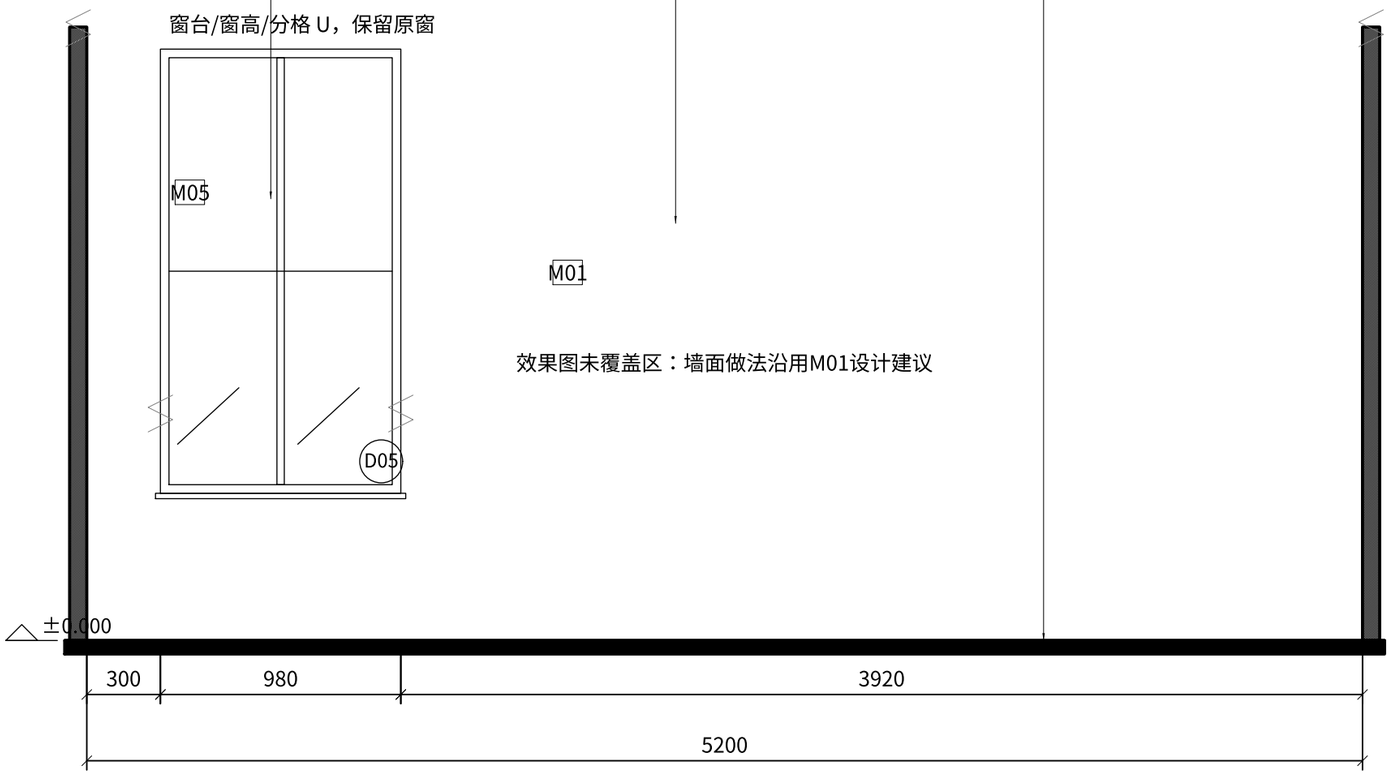

效果图未覆盖区：墙面做法沿用M01设计建议

主图尺寸：P为原图，D为设计建议；门窗竖向未确认项见右栏

01 / 材料及做法

M01 墙面涂装
M02 木作饰面
M03 织物/软饰面
M06 地板及踢脚
编码对应GE-01材料表。

02 / 节点索引

D05 窗口与木饰面收边
D09 踢脚及转角

03 / 原图与效果依据

P45–50效果意向。
原DXF几何见GE-02。

04 / 待协调事项


吊顶完成净高H、材料样板及固定条件待确认。

P 原图	平面5200×3790；深3790由墙线几何读取。
I 意向	P45–50；图面未覆盖部位列为建议，不冒称效果图已有。
D 深化	南墙不增设无源门洞；未覆盖墙面仅提出面层建议。
U 待核	吊顶净高、门窗竖向、饰面选型及连接条件，详GE-00。

西湖豪庭 2#2单元603	卧室深化 / R04	EL-03	1:25	待签审

主卧 / D 向立面

朝原平面左侧 · 平面范围P；构造及新增高度D；未知总高H不补成实测值

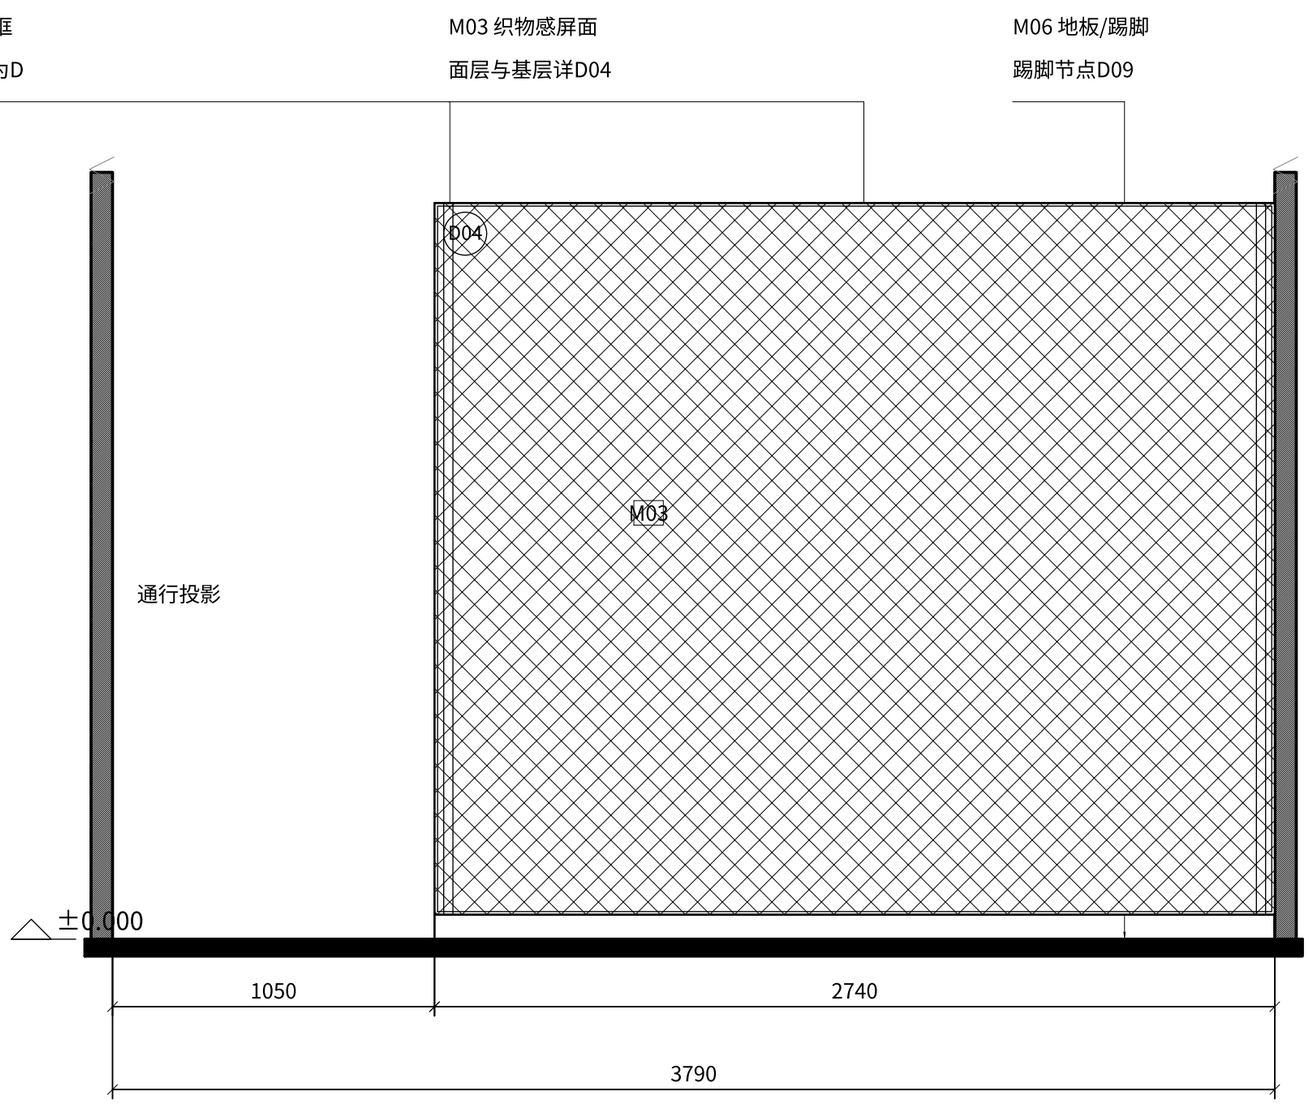

01 / 材料及做法

M01 墙面涂装
M02 木作饰面
M03 织物/软饰面
M06 地板及踢脚
编码对应GE-01材料表。

02 / 节点索引

D04 织物板与木边框
D02 顶部收口，H待核

03 / 原图与效果依据

P45–50效果意向。
原DXF几何见GE-02。


04 / 待协调事项

吊顶完成净高H、材料样板及固定条件待确认。

P 原图	平面5200×3790；深3790由墙线几何读取。
I 意向	P45–50；图面未覆盖部位列为建议，不冒称效果图已有。
D 深化	织物屏面及木边框按P47意向深化；屏高2400为D。
U 待核	吊顶净高、门窗竖向、饰面选型及连接条件，详GE-00。

次卧（效果图称老人房） / A 向立面

朝原平面上侧 · 平面范围P；构造及新增高度D；未知总高H不补成实测值

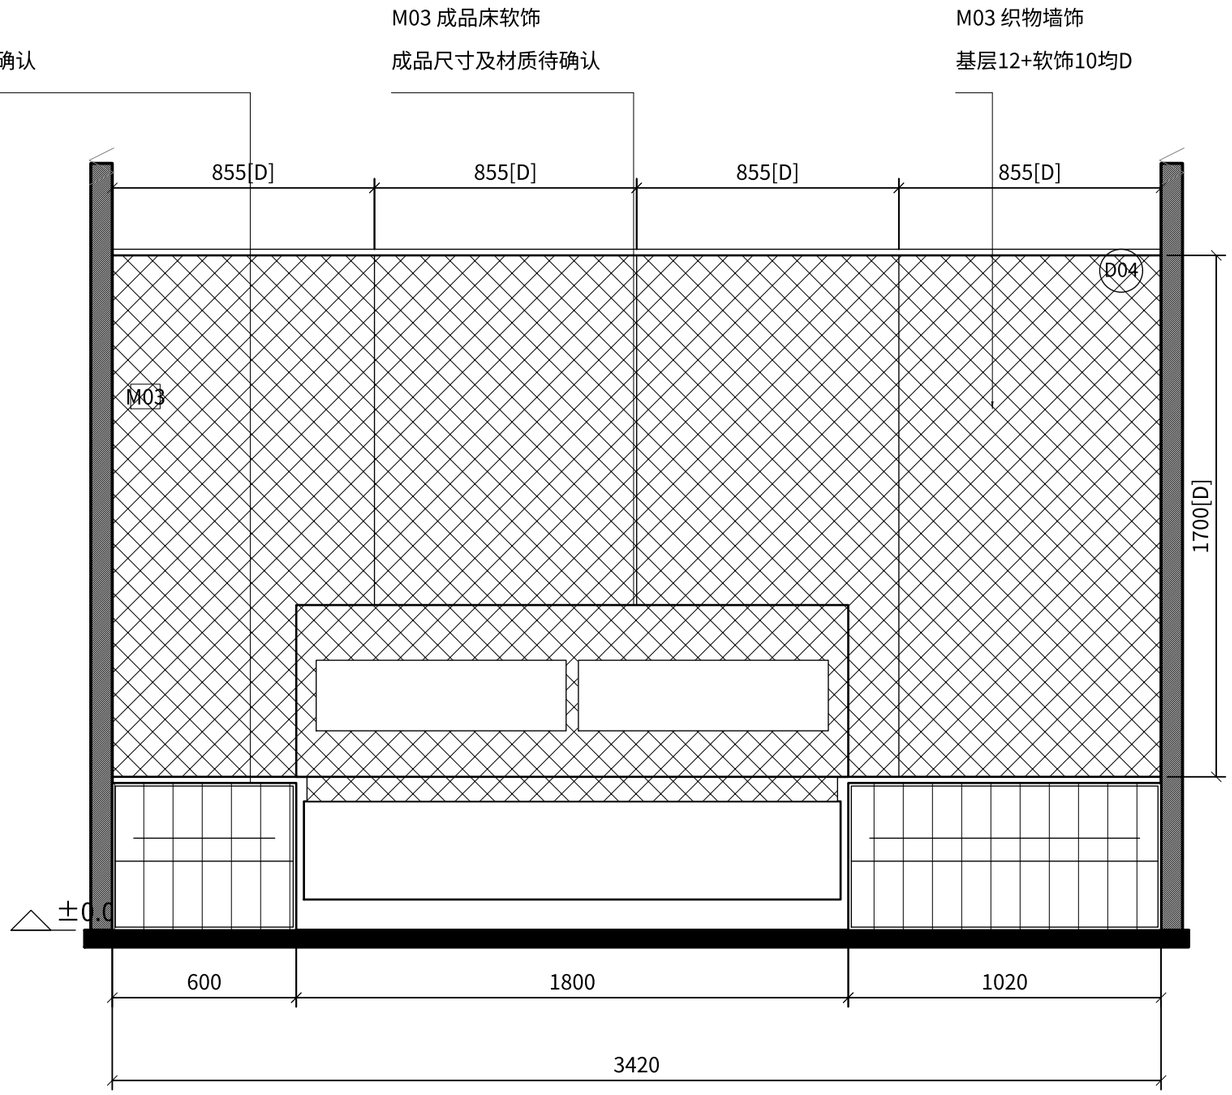

01 / 材料及做法

M01 墙面涂装
M02 木作饰面
M03 织物/软饰面
M06 地板及踢脚
编码对应GE-01材料表。

02 / 节点索引

D01/D02 柜脚、柜顶
D04 软饰面与木作交接

03 / 原图与效果依据

P54–56效果意向。
原DXF几何见GE-02。


04 / 待协调事项

吊顶完成净高H、材料样板及固定条件待确认。

P 原图	3420=600+1800+1020；3430=2100+1030+300。
I 意向	P54–56；图面未覆盖部位列为建议，不冒称效果图已有。
D 深化	软饰面从500至2200，四模数855；灯槽位置为D。
U 待核	吊顶净高、门窗竖向、饰面选型及连接条件，详GE-00。

次卧（效果图称老人房） / B 向立面

朝原平面右侧 · 平面范围P；构造及新增高度D；未知总高H不补成实测值

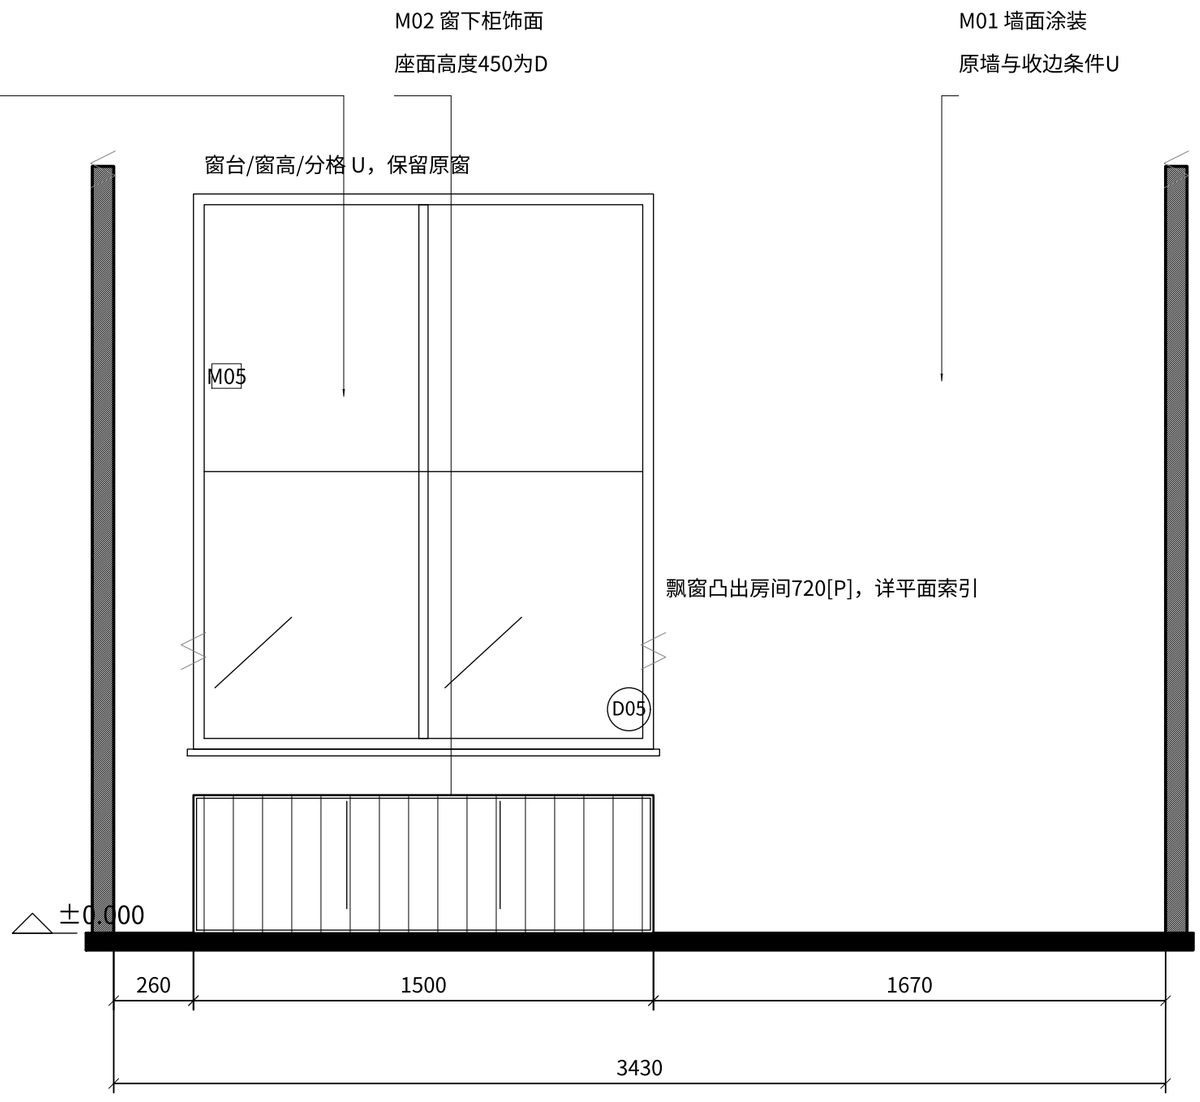

01 / 材料及做法

M01 墙面涂装
M02 木作饰面
M03 织物/软饰面
M06 地板及踢脚
编码对应GE-01材料表。

02 / 节点索引

D05 窗套基层与饰面
D09 座面邻墙收口

03 / 原图与效果依据

P54–56效果意向。
原DXF几何见GE-02。

04 / 待协调事项

吊顶完成净高H、材料样板及固定条件待确认。

P 原图	3420=600+1800+1020；3430=2100+1030+300。
I 意向	P54–56；图面未覆盖部位列为建议，不冒称效果图已有。
D 深化	飘窗储物座面450为D；开扇、原窗窗台及承托需复核。
U 待核	吊顶净高、门窗竖向、饰面选型及连接条件，详GE-00。

次卧（效果图称老人房） / C 向立面

朝原平面下侧 · 平面范围P；构造及新增高度D；未知总高H不补成实测值

M02 木色门饰面


门扇尺寸与选型U

M09 哑光柜门

面层及色号为D建议

M06 地板/踢脚

节点D09

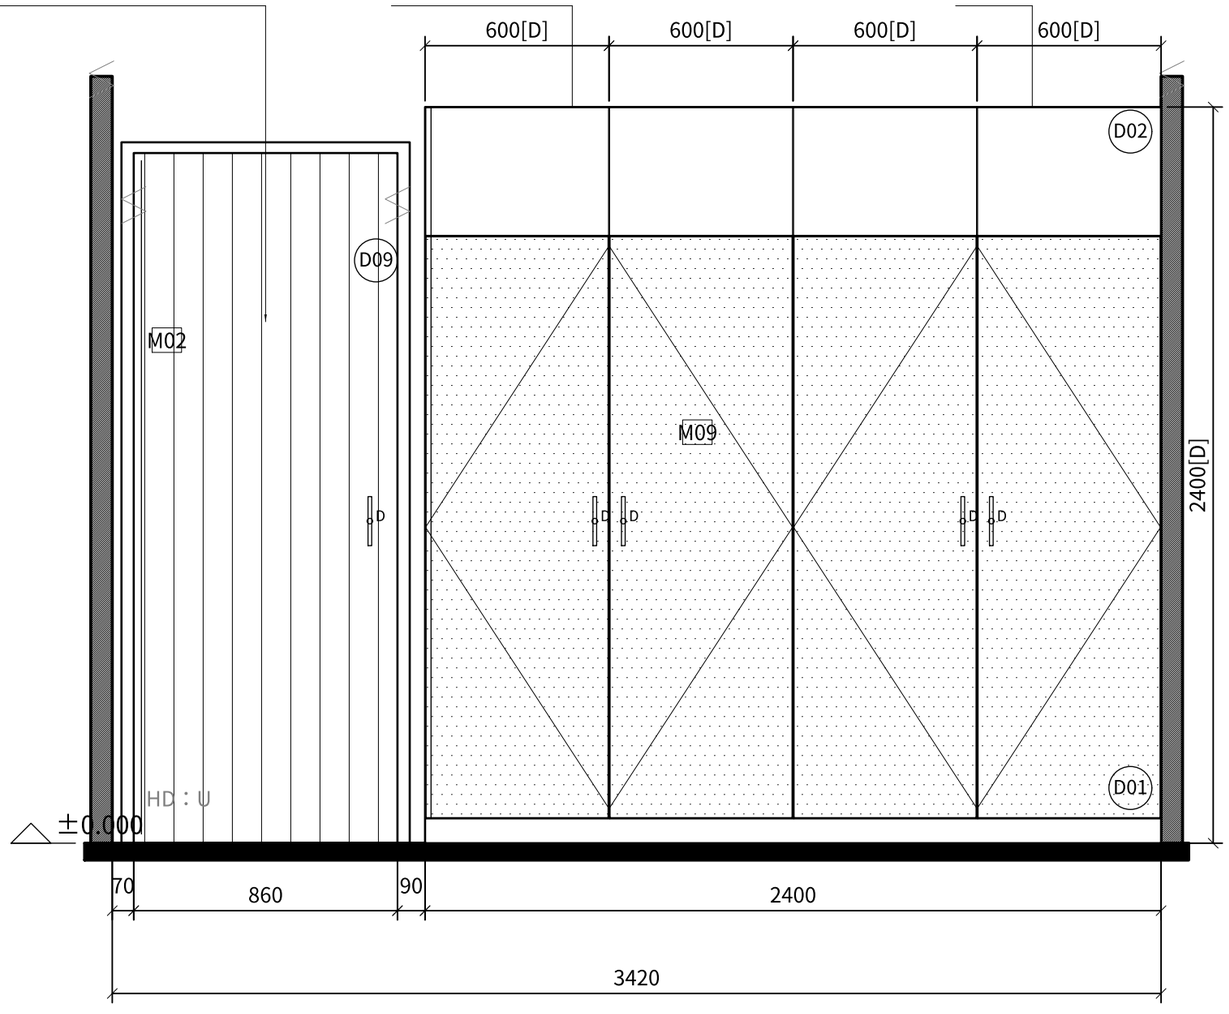

01 / 材料及做法

M01 墙面涂装
M02 木作饰面
M03 织物/软饰面
M06 地板及踢脚
编码对应GE-01材料表。

02 / 节点索引

JB-03 薄柜内部与剖面
D01/D03 柜脚和门缝

03 / 原图与效果依据

P54–56效果意向。
原DXF几何见GE-02。

04 / 待协调事项


吊顶完成净高H、材料样板及固定条件待确认。

P 原图	3420=600+1800+1020；3430=2100+1030+300。
I 意向	P54–56；图面未覆盖部位列为建议，不冒称效果图已有。
D 深化	薄柜深300，内部以层板储物为主；不作常规挂衣柜。
U 待核	吊顶净高、门窗竖向、饰面选型及连接条件，详GE-00。

西湖豪庭 2#2单元603	卧室深化 / R04	EL-07	1:20	待签审

次卧（效果图称老人房） / D 向立面

朝原平面左侧 · 平面范围P；构造及新增高度D；未知总高H不补成实测值

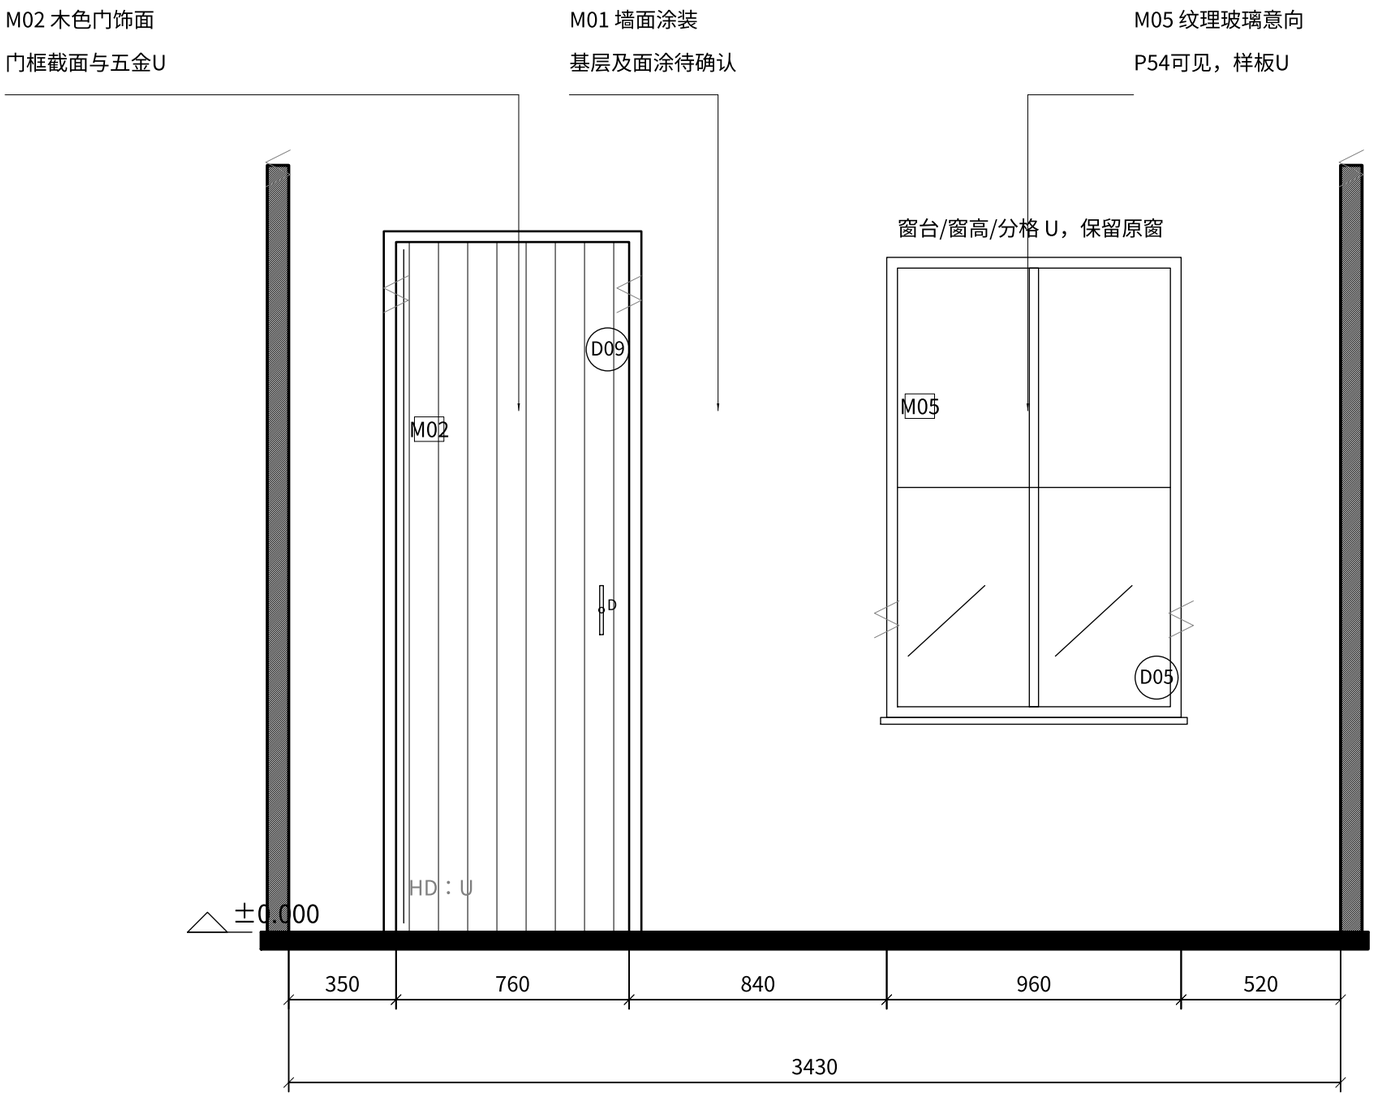

P 原图	3420=600+1800+1020；3430=2100+1030+300。
I 意向	P54–56；图面未覆盖部位列为建议，不冒称效果图已有。
D 深化	内窗竖向及分格U；以P54纹理玻璃意向深化窗框收口。
U 待核	吊顶净高、门窗竖向、饰面选型及连接条件，详GE-00。

01 / 材料及做法

M01 墙面涂装
M02 木作饰面
M03 织物/软饰面
M06 地板及踢脚
编码对应GE-01材料表。

02 / 节点索引

D05 玻璃窗框与墙面
D09 门套、踢脚交接

03 / 原图与效果依据

P54–56效果意向。
原DXF几何见GE-02。

04 / 待协调事项

吊顶完成净高H、材料样板及固定条件待确认。

西湖豪庭 2#2单元603	卧室深化 / R04	EL-08	1:20	待签审

女儿房 / A 向立面

朝原平面上侧 · 平面范围P；构造及新增高度D；未知总高H不补成实测值

M04 粉色织物感面


斜顶面层按P60意向

M02 灯光开放格

背板退后，层板在前

M09 哑光柜门

柜身木色与门面区分

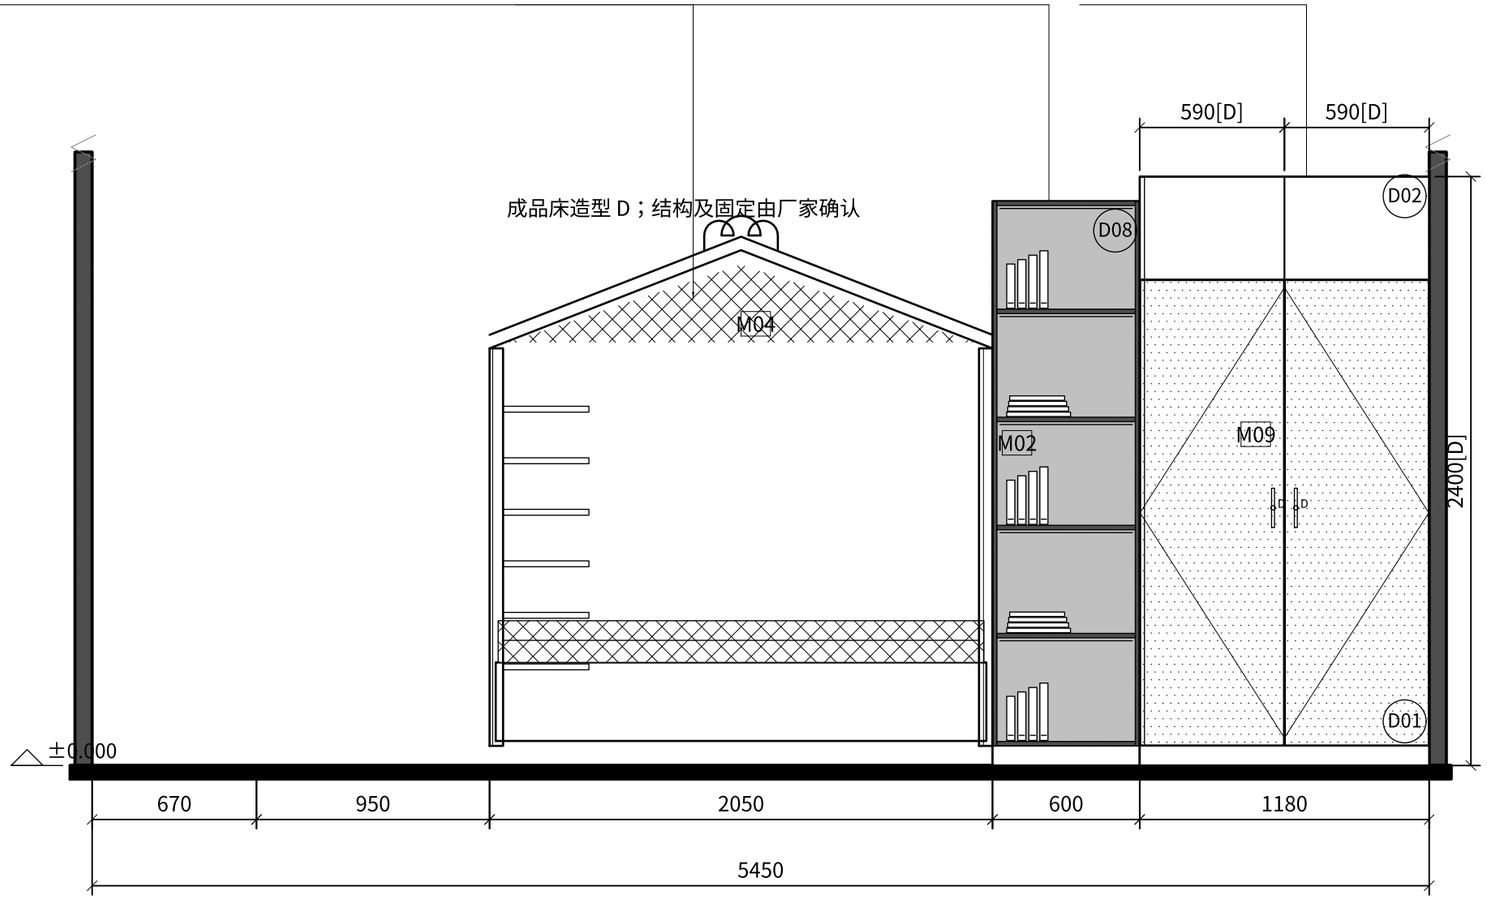

主图尺寸：P为原图，D为设计建议；门窗竖向未确认项见右栏

01 / 材料及做法

M01 墙面涂装
M02 木作饰面
M03 织物/软饰面
M06 地板及踢脚
编码对应GE-01材料表。

02 / 节点索引

D08 开放层板灯槽
D01/D02 杂物柜底顶

03 / 原图与效果依据

P60–63效果意向。
原DXF几何见GE-02。


04 / 待协调事项

吊顶完成净高H、材料样板及固定条件待确认。 儿童床成品尺寸、攀爬及防倾覆固定需厂家图。

P 原图	5450=670+950+2050+600+1180；3010=1500+890+620。
I 意向	P60–63；图面未覆盖部位列为建议，不冒称效果图已有。
D 深化	杂物柜原平面深300；床侧屋形与攀爬架按P60意向，非受力图。
U 待核	吊顶净高、门窗竖向、饰面选型及连接条件，详GE-00。

女儿房 / B 向立面

朝原平面右侧 · 平面范围P；构造及新增高度D；未知总高H不补成实测值

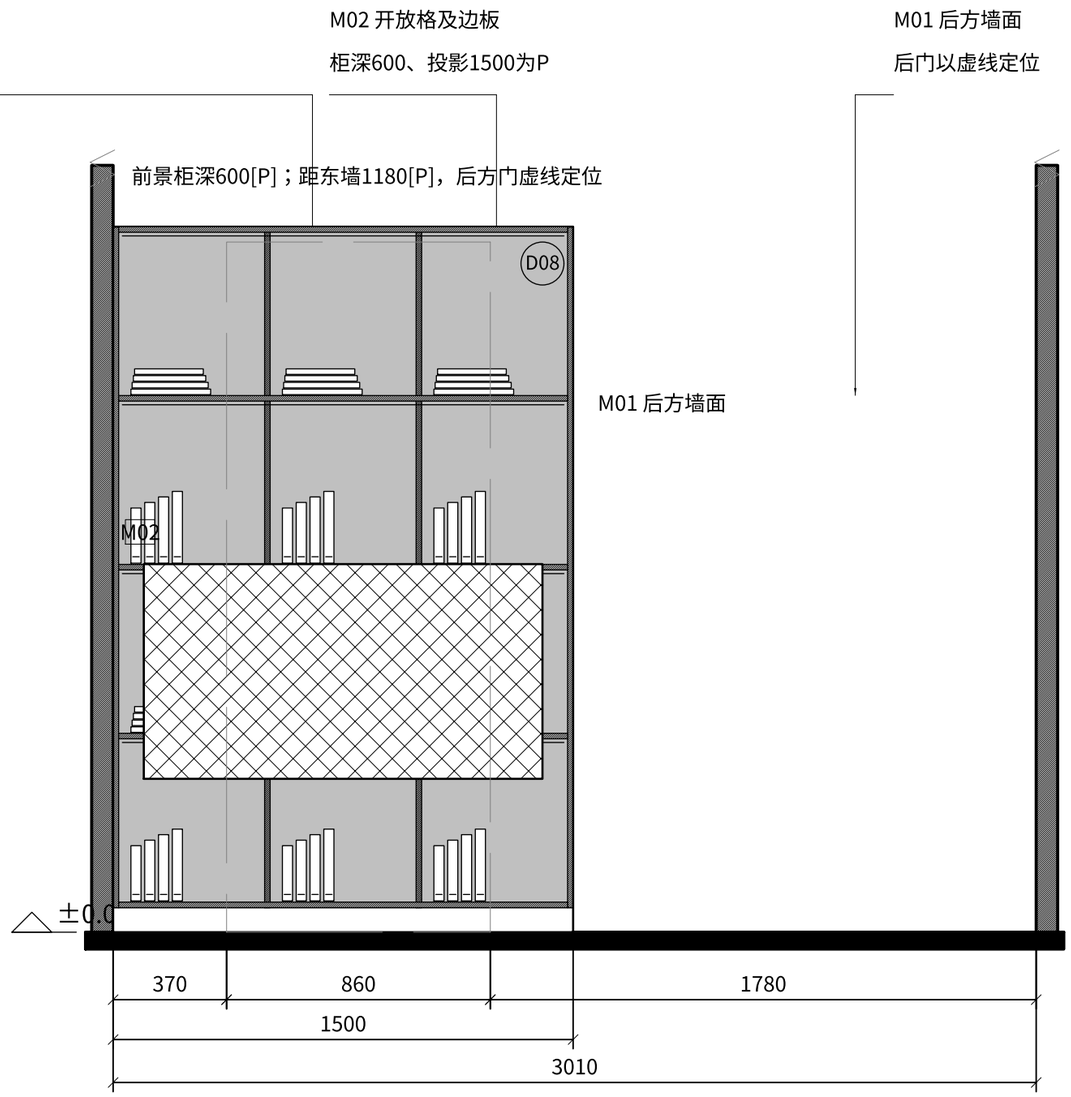

01 / 材料及做法

M01 墙面涂装
M02 木作饰面
M03 织物/软饰面
M06 地板及踢脚
编码对应GE-01材料表。

02 / 节点索引

D09 门套及墙脚
D04 床头饰面边缘

03 / 原图与效果依据

P60–63效果意向。
原DXF几何见GE-02。


04 / 待协调事项

吊顶完成净高H、材料样板及固定条件待确认。

P 原图	5450=670+950+2050+600+1180；3010=1500+890+620。
I 意向	P60–63；图面未覆盖部位列为建议，不冒称效果图已有。
D 深化	床头整合体前景遮挡后门；改为开放格及软饰面，拟高2300[D]。
U 待核	吊顶净高、门窗竖向、饰面选型及连接条件，详GE-00。

女儿房 / C 向立面

朝原平面下侧 · 平面范围P；构造及新增高度D；未知总高H不补成实测值

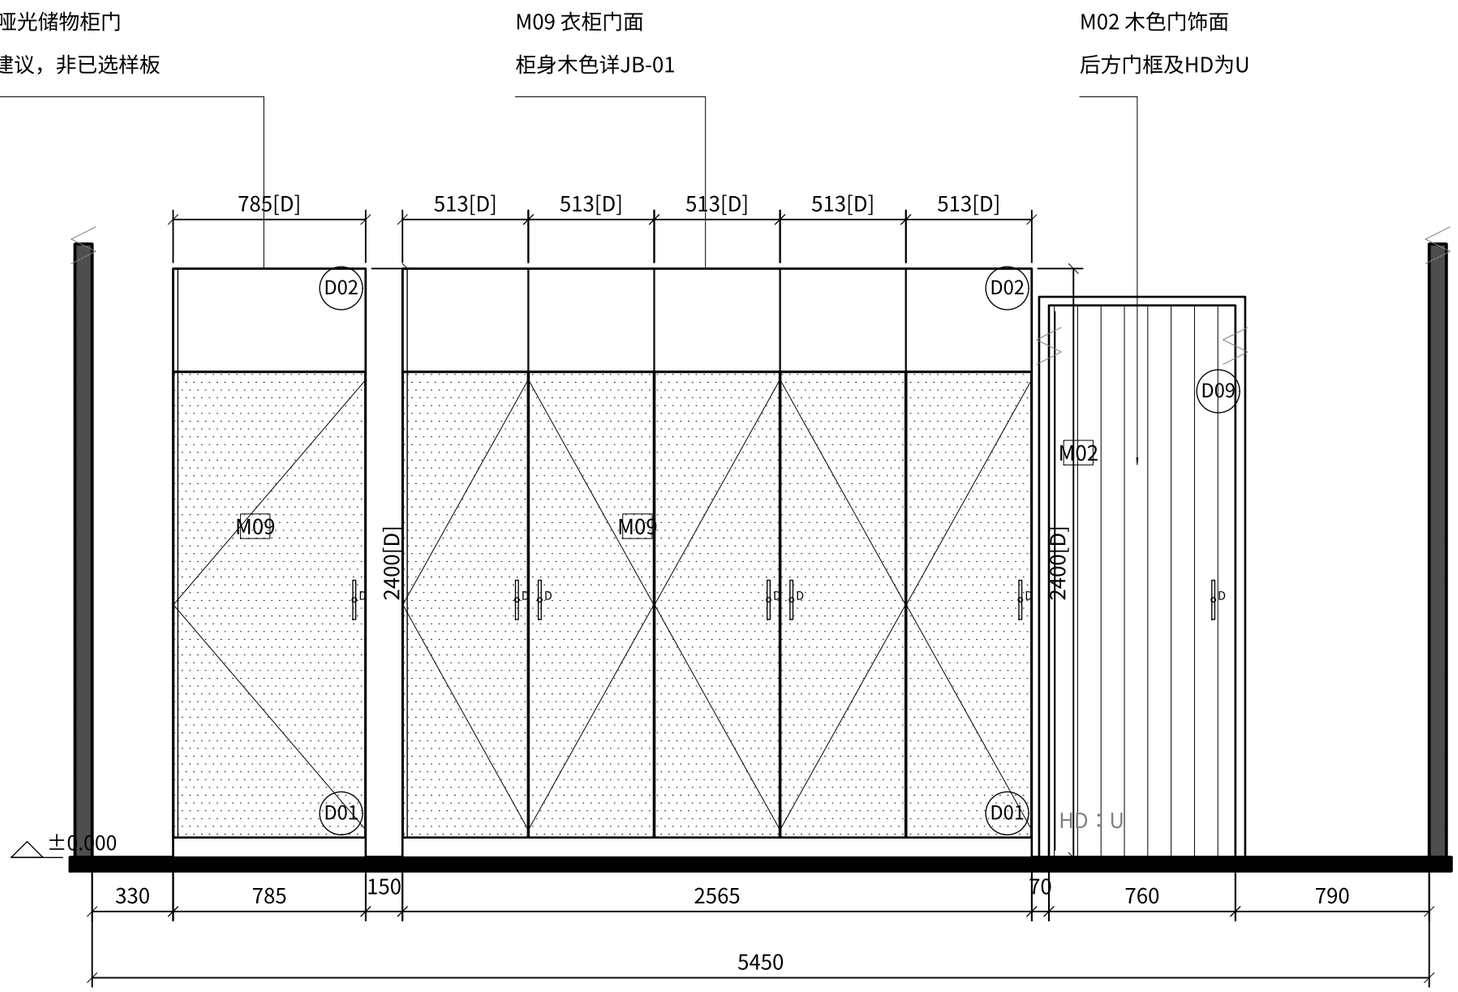

主图尺寸：P为原图，D为设计建议；门窗竖向未确认项见右栏

01 / 材料及做法

M01 墙面涂装
M02 木作饰面
M03 织物/软饰面
M06 地板及踢脚
编码对应GE-01材料表。

02 / 节点索引

JB-01 衣柜内部与侧剖
D01/D02/D03 柜脚、顶、门缝

03 / 原图与效果依据

P60–63效果意向。
原DXF几何见GE-02。

04 / 待协调事项

吊顶完成净高H、材料样板及固定条件待确认。

P 原图	5450=670+950+2050+600+1180；3010=1500+890+620。
I 意向	P60–63；图面未覆盖部位列为建议，不冒称效果图已有。
D 深化	衣柜5个513定位模数；门板缝、内部净宽与剖面详JB-01。
U 待核	吊顶净高、门窗竖向、饰面选型及连接条件，详GE-00。


女儿房 / D 向立面

朝原平面左侧 · 平面范围P；构造及新增高度D；未知总高H不补成实测值

M02 木色台板
哑光抽面与木板分开

M03 织物感座垫
座垫70为D建议

M05 原窗玻璃
窗线在台柜之后

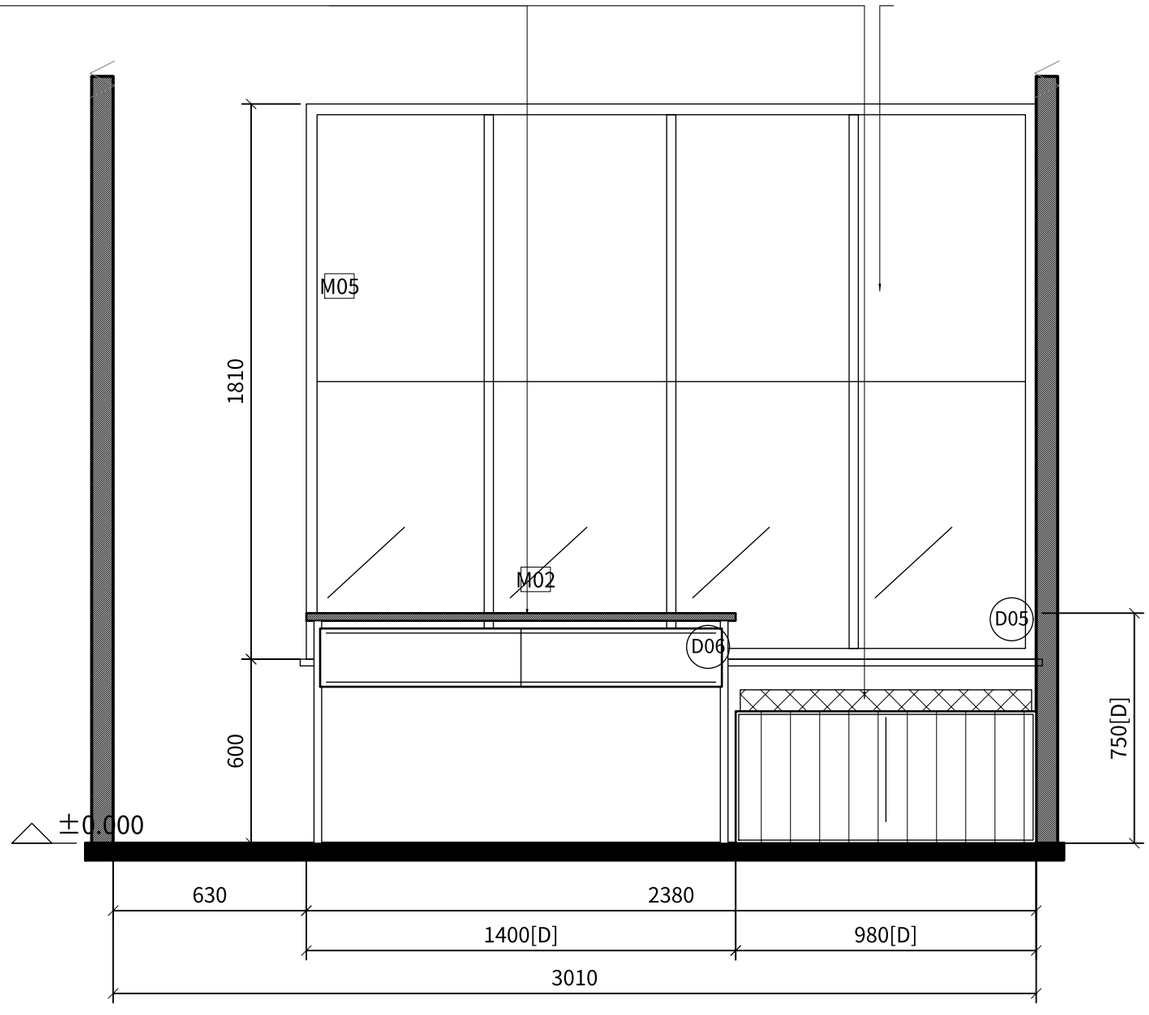

01 / 材料及做法

M01 墙面涂装
M02 木作饰面
M03 织物/软饰面
M06 地板及踢脚
编码对应GE-01材料表。

02 / 节点索引

D06 桌台/座面/窗台协调
D07 窗帘槽及检修

03 / 原图与效果依据

P60–63效果意向。
原DXF几何见GE-02。

04 / 待协调事项

桌面750[D]高于原窗台600[P]共150；窗扇开启未确认，不可下单。

P 原图	5450=670+950+2050+600+1180；3010=1500+890+620。
I 意向	P60–63；图面未覆盖部位列为建议，不冒称效果图已有。
D 深化	按P63拆为桌1400+窗边座980[D]，合计保留原轮廓2380[P]。
U 待核	吊顶净高、门窗竖向、饰面选型及连接条件，详GE-00。

男孩房 / A 向立面

朝原平面上侧 · 平面范围P；构造及新增高度D；未知总高H不补成实测值

M02 木色门饰面


门框及五金规格U

M08 蓝色哑光意向

转角归属及做法D

M02 玩具矮柜

退后背板与前置层板

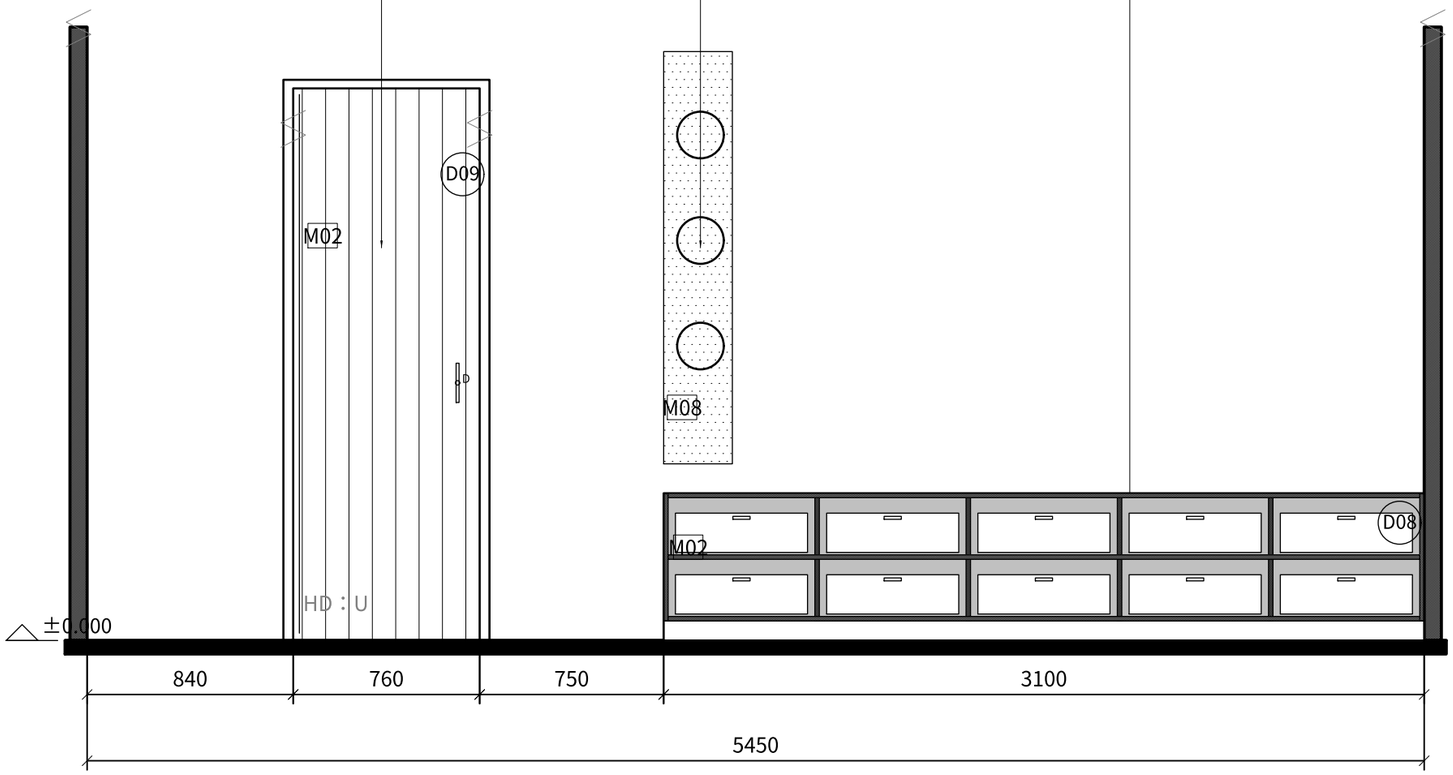

主图尺寸：P为原图，D为设计建议；门窗竖向未确认项见右栏

01 / 材料及做法

M01 墙面涂装
M02 木作饰面
M03 织物/软饰面
M06 地板及踢脚
编码对应GE-01材料表。

02 / 节点索引

JB-03 玩具柜分格
D01/D08 柜底及层板

03 / 原图与效果依据

P65–67效果意向。
原DXF几何见GE-02。

04 / 待协调事项

吊顶完成净高H、材料样板及固定条件待确认。

P 原图	北侧柜后墙基准深2870（几何）；2690链至柜内线，不作净深。
I 意向	P65–67；图面未覆盖部位列为建议，不冒称效果图已有。
D 深化	玩具柜高600[D]；3100原跨度不变。圆饰及蓝色面位置为D意向。
U 待核	吊顶净高、门窗竖向、饰面选型及连接条件，详GE-00。


男孩房 / B 向立面

朝原平面右侧 · 平面范围P；构造及新增高度D；未知总高H不补成实测值

M02 木色门饰面
门套邻柜余量20[P]

M09 哑光衣柜门
色样及五金U

M06 地板/踢脚
柜脚与地面详D01

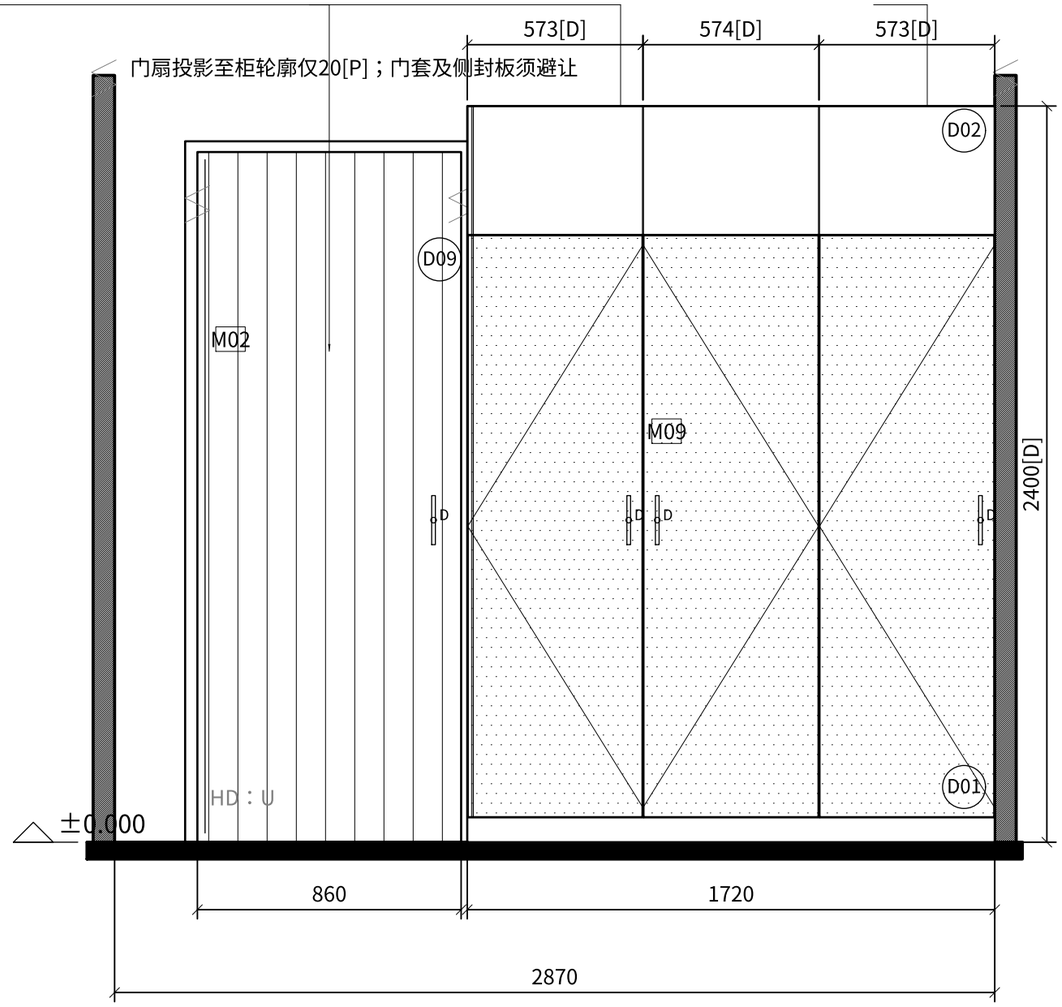

01 / 材料及做法

M01 墙面涂装
M02 木作饰面
M03 织物/软饰面
M06 地板及踢脚
编码对应GE-01材料表。

02 / 节点索引

JB-02 衣柜内部和门套冲突
D03 门板/侧封板平剖

03 / 原图与效果依据

P65–67效果意向。
原DXF几何见GE-02。

04 / 待协调事项

吊顶完成净高H、材料样板及固定条件待确认。

P 原图	北侧柜后墙基准深2870（几何）；2690链至柜内线，不作净深。
I 意向	P65–67；图面未覆盖部位列为建议，不冒称效果图已有。
D 深化	三定位模数573/574/573；柜侧与门套20余量不足，详JB-02。
U 待核	吊顶净高、门窗竖向、饰面选型及连接条件，详GE-00。

男孩房 / C 向立面

朝原平面下侧 · 平面范围P；构造及新增高度D；未知总高H不补成实测值

M04 绿色织物感面


斜顶与木框分材质

M03 成品床软饰

成品厂家确认

M02 木色桌板

抽面为M09建议

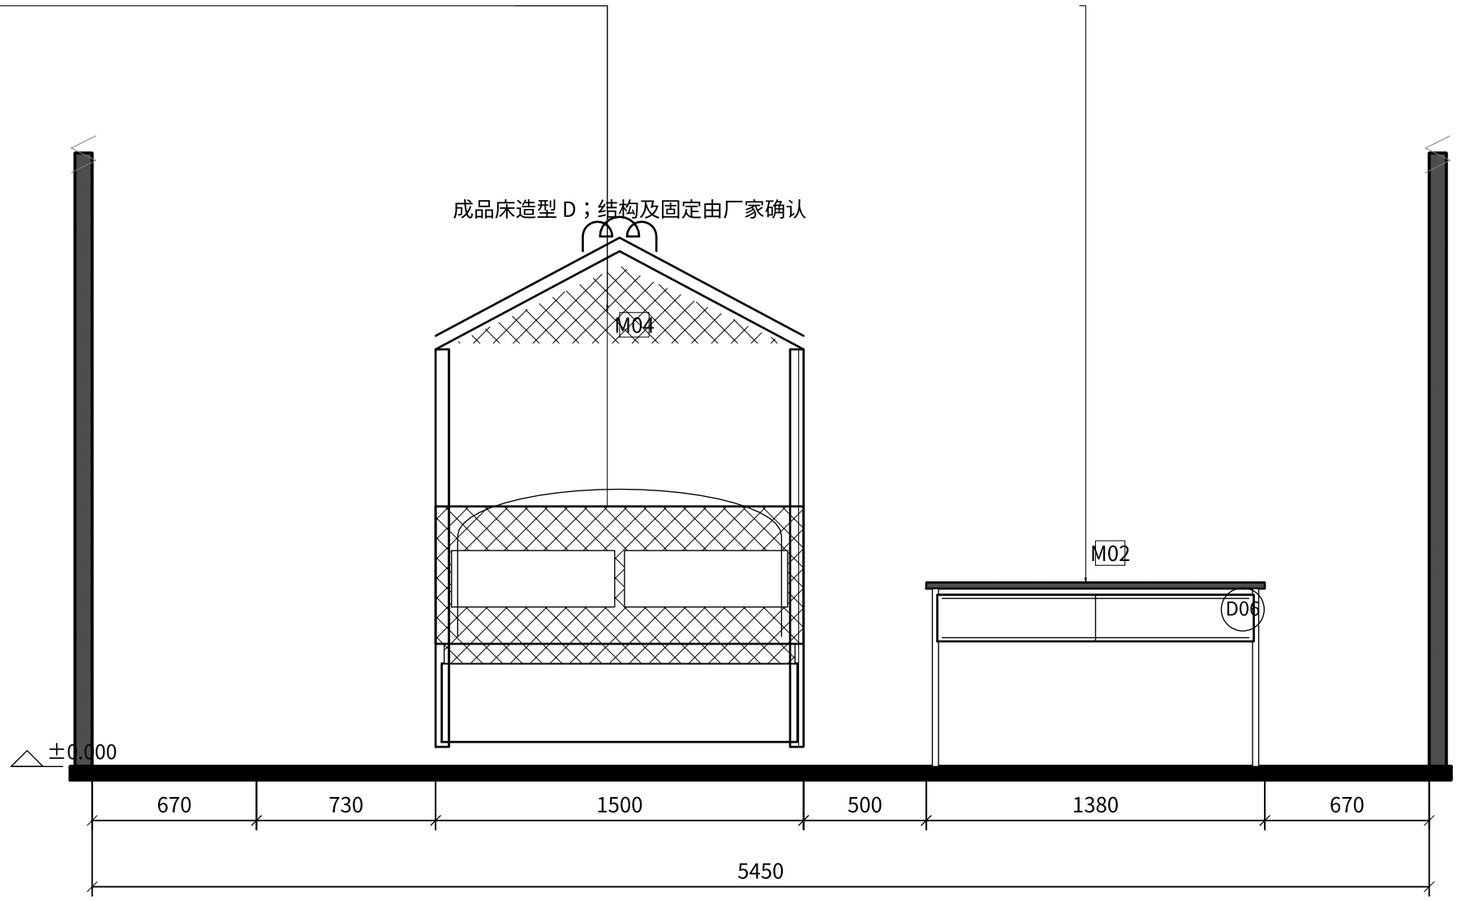

主图尺寸：P为原图，D为设计建议；门窗竖向未确认项见右栏

01 / 材料及做法

M01 墙面涂装
M02 木作饰面
M03 织物/软饰面
M06 地板及踢脚
编码对应GE-01材料表。

02 / 节点索引

D06 书桌边部及支承
D04 床头软饰面边框

03 / 原图与效果依据

P65–67效果意向。
原DXF几何见GE-02。

04 / 待协调事项

吊顶完成净高H、材料样板及固定条件待确认。 成品床安装及防倾覆由厂家深化。

P 原图	北侧柜后墙基准深2870（几何）；2690链至柜内线，不作净深。
I 意向	P65–67；图面未覆盖部位列为建议，不冒称效果图已有。
D 深化	桌回折段1380[P]，保留与主体2670桌段的转角搭接关系。
U 待核	吊顶净高、门窗竖向、饰面选型及连接条件，详GE-00。

男孩房 / D 向立面

朝原平面左侧 · 平面范围P；构造及新增高度D；未知总高H不补成实测值

M02 木色台板


板厚25为D建议

M09 哑光抽面

遮挡背景窗线

M05 原窗玻璃

开启范围仍待复核

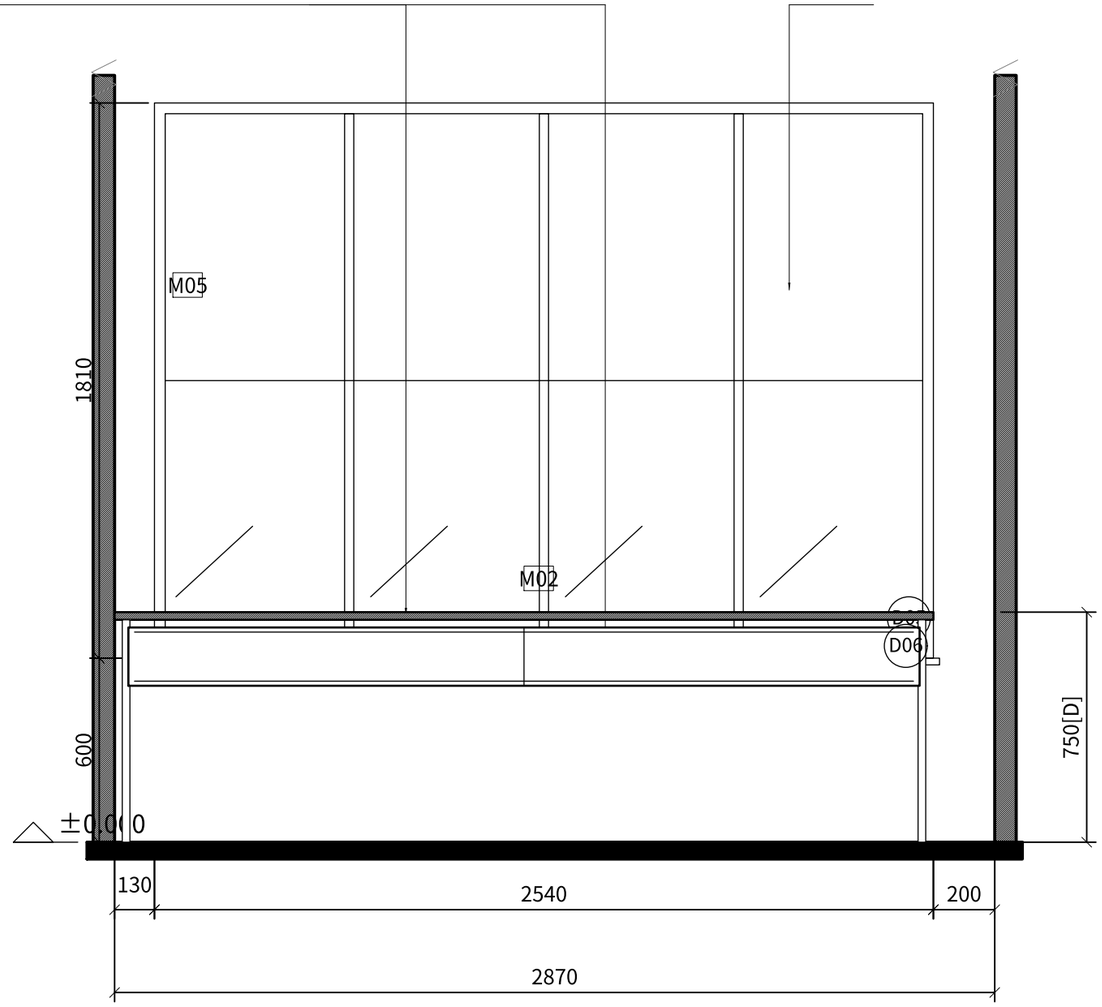

01 / 材料及做法

M01 墙面涂装
M02 木作饰面
M03 织物/软饰面
M06 地板及踢脚
编码对应GE-01材料表。

02 / 节点索引

D06 原窗与台面高差
D07 窗帘盒及检修

03 / 原图与效果依据

P65–67效果意向。
原DXF几何见GE-02。

04 / 待协调事项


桌高750[D]与窗台600[P]相差150，开扇范围待核；CH2920不作吊顶净高。

P 原图	北侧柜后墙基准深2870（几何）；2690链至柜内线，不作净深。
I 意向	P65–67；图面未覆盖部位列为建议，不冒称效果图已有。
D 深化	柜后墙深2870；桌及柜前基准2670；不混作同一净深。
U 待核	吊顶净高、门窗竖向、饰面选型及连接条件，详GE-00。

西湖豪庭 2#2单元603	卧室深化 / R04	EL-16	1:20	待签审


女儿房衣柜 / 内部及侧剖

P外轮廓保留；板厚、净格、内部功能均为D建议；门板下料需柜厂复核

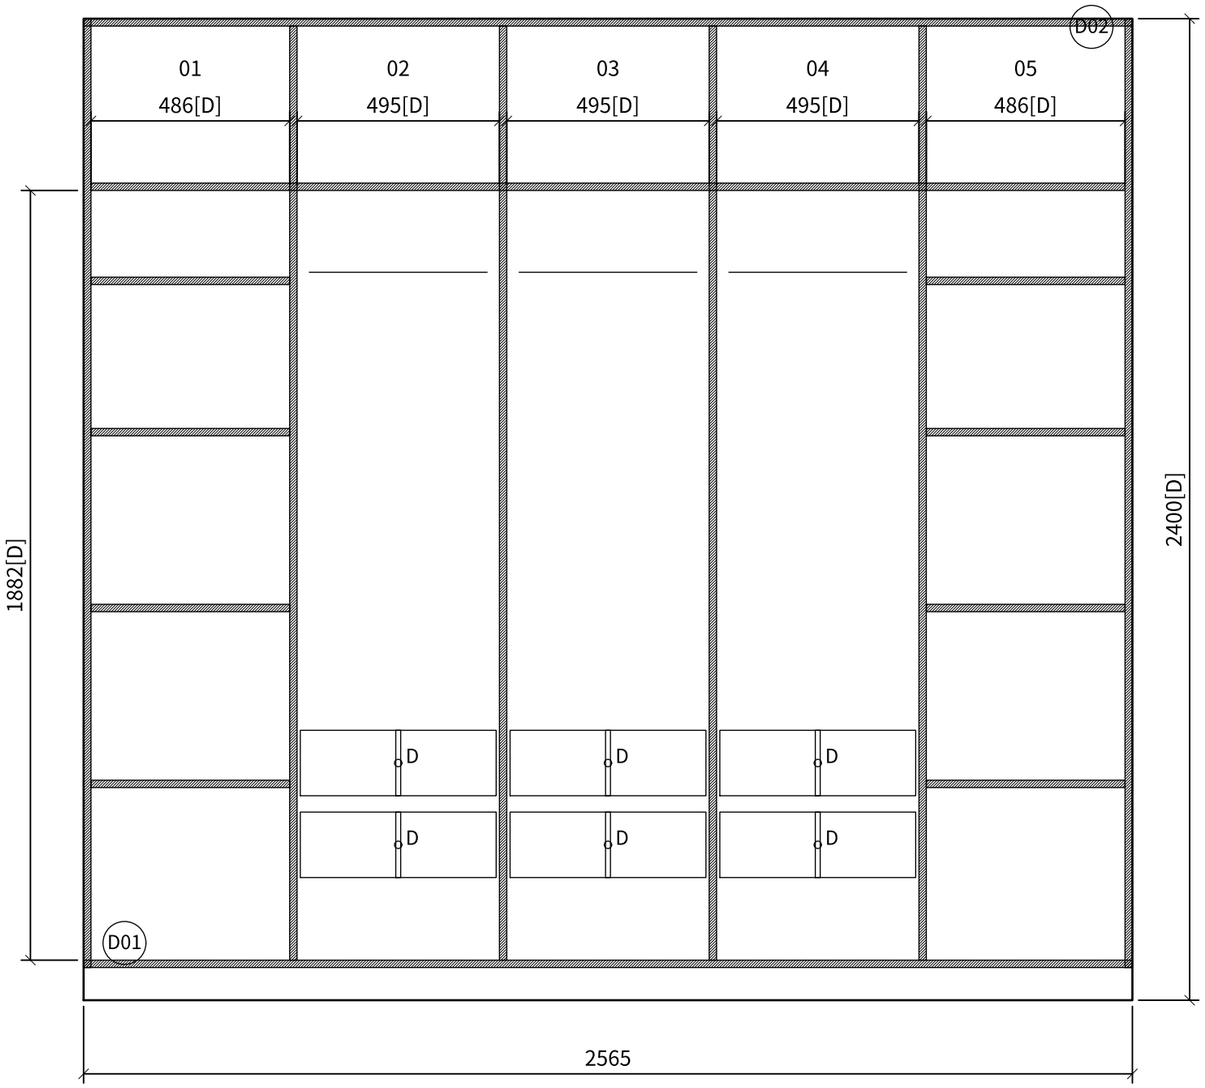

01 内部展开 1:15

背板9、前缝3、门板18均D

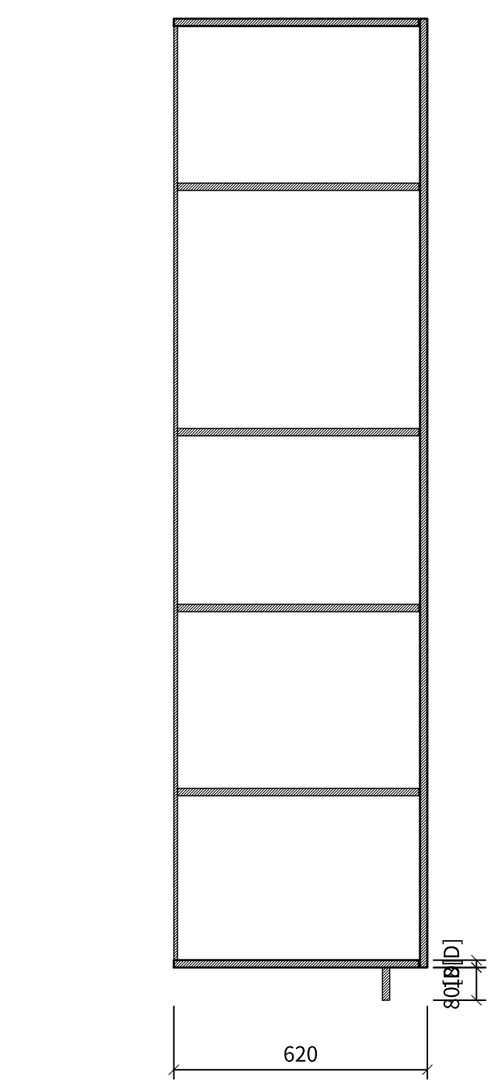

02 侧剖 1:15


板厚18[D]。
上口净空384[D]。
下柜净高1882[D]。
背板9[D]。
门板18[D]。
前缝3[D]。
层板、挂杆与抽屉均属建议。
固定件、载荷、五金选型另核。
H未定，柜顶收口可调。

外轮廓P	2565 × 620	仅外宽、进深为P；高2400为D
净格D	486 / 495 / 495 / 495 / 486	净格总和 + 6块18板 = 2565

西湖豪庭 2#2单元603	卧室深化 / R04	JB-01	1:15	待签审


男孩房衣柜 / 内部及侧剖

P外轮廓保留；板厚、净格、内部功能均为D建议；门板下料需柜厂复核

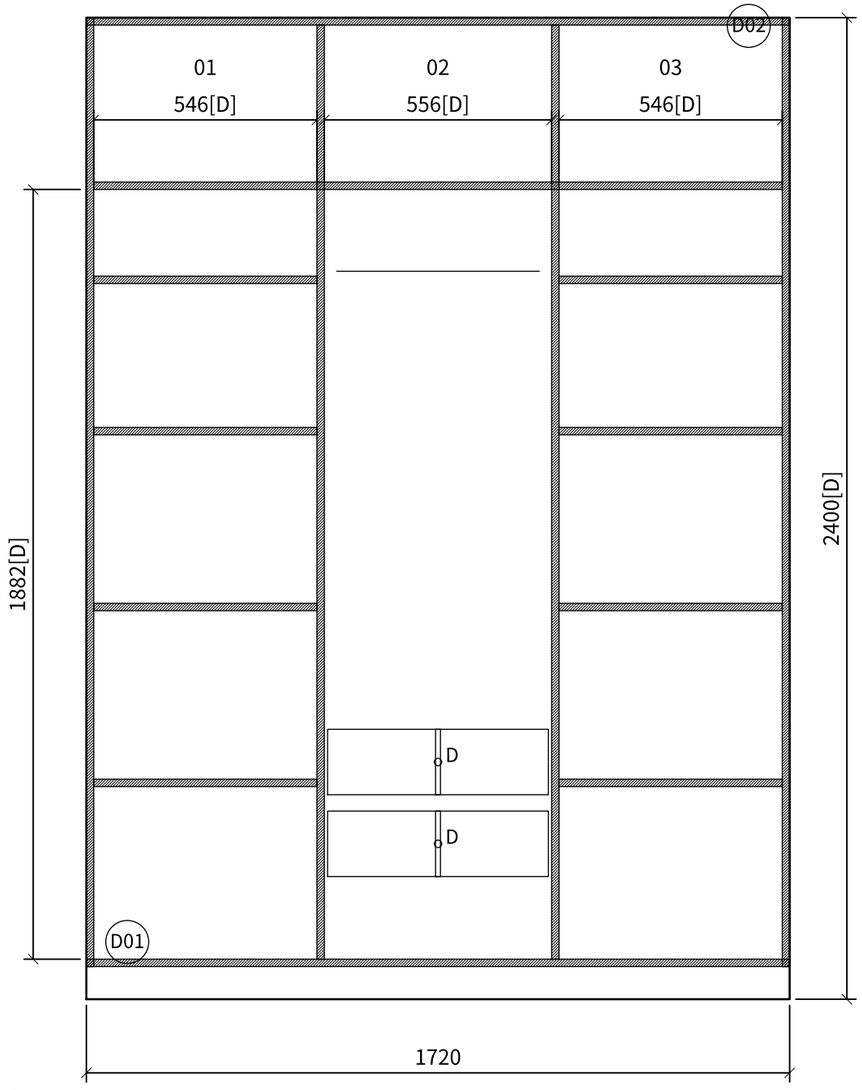

01 内部展开 1:15

背板9、前缝3、门板18均D

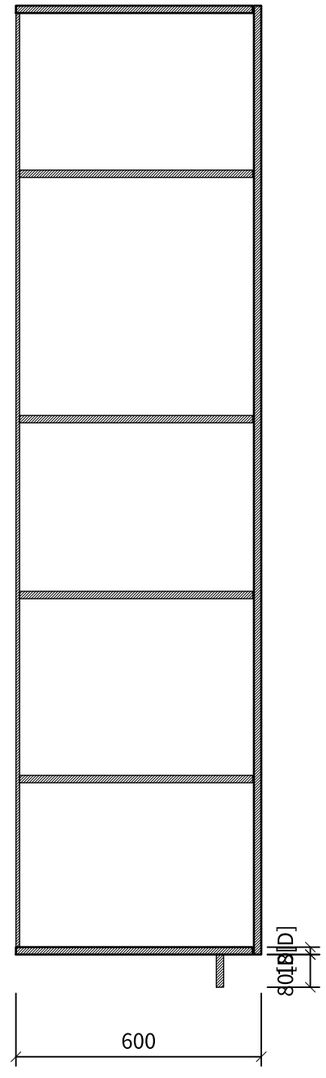
600
18[D]

02 侧剖 1:15

板厚18[D]。
上口净空384[D]。
下柜净高1882[D]。
背板9[D]。
门板18[D]。
前缝3[D]。
层板、挂杆与抽屉均属建议。
固定件、载荷、五金选型另核。
H未定，柜顶收口可调。


门扇与柜轮廓相距20[P]。
该余量不足以直接确定门套和侧封板，须现场协调。

外轮廓P	1720 × 600	仅外宽、进深为P；高2400为D
净格D	546 / 556 / 546	净格总和 + 4块18板 = 1720


西湖豪庭 2#2单元603	卧室深化 / R04	JB-02	1:15	待签审

薄柜与玩具柜 / 内部功能深化

薄柜进深300；玩具柜源图进深200，收纳篮选型可能需要另改进深

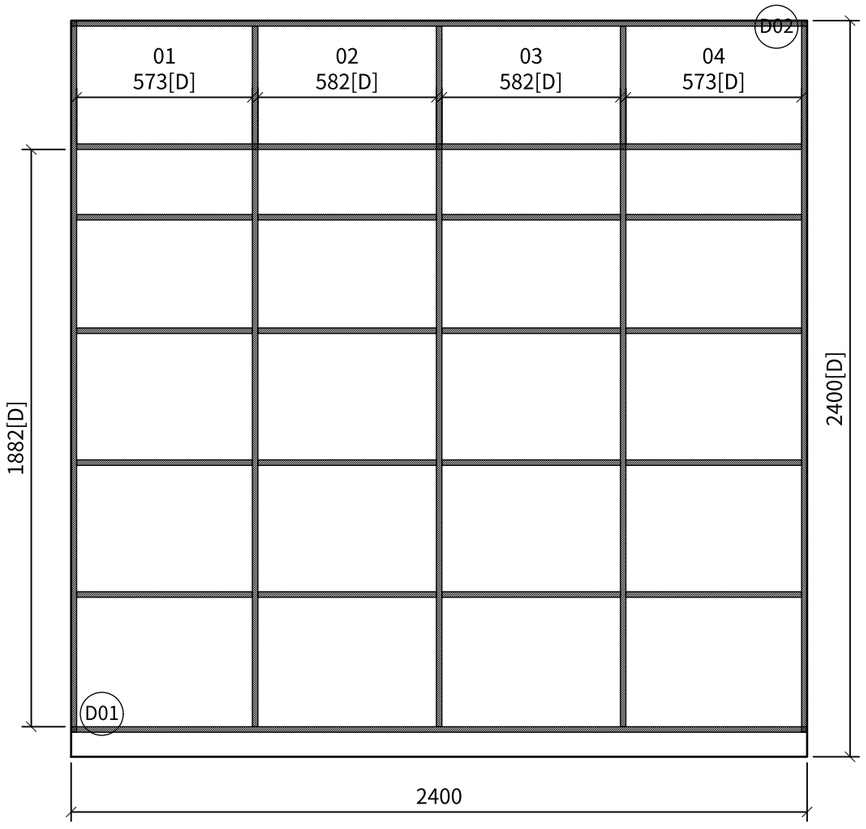

次卧薄柜内部 / 1:20 / 仅层板储物

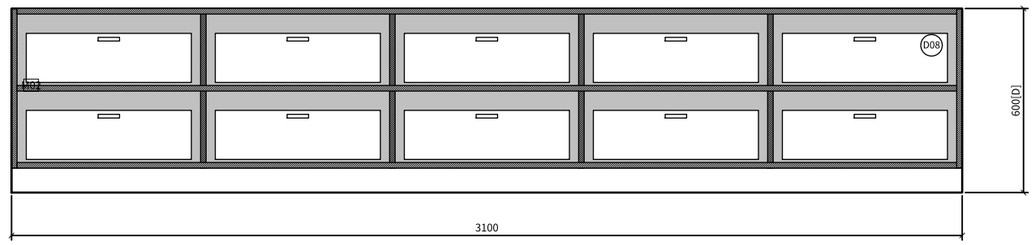

玩具矮柜 / 1:20

源平面深200[P]，本版不擅自改深以容纳效果图篮筐。
若保留该进深，仅适合薄书或浅件；需按篮筐实物与通行净距再定。
两层与分格属D；层板18，跨距及固定按实际载荷校核。

薄柜：4个600定位模数；净格573/582/582/573[D]，两侧及隔板均18[D]。
玩具柜：外宽3100[P]；五格净宽均598.4[D]，共6块18板，闭合3100。


西湖豪庭 2#2单元603	卧室深化 / R04	JB-03	详见各图	待签审

节点深化 / D01 · D02

所有未标P的节点尺寸与连接构造均为D；原基层及未确认条件标U

D01 柜底 / 调节脚 / 踢脚


比例 1:5 / 模型1:1 mm

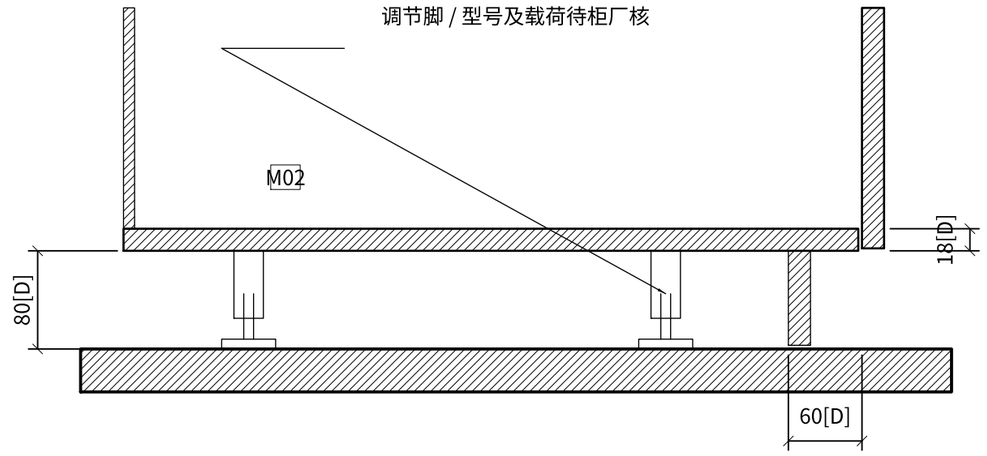

底板18、门板18、踢脚80均D。
踢脚退后60[D]；调节脚形态仅示意。
底板经调节脚传力至完成地面；不可只靠踢脚板承托。
调节脚及底板承载、固定件型号/间距由柜厂复核。
原地面及完成厚度U，现场找平后复尺。

D02 柜顶 / 可调封板 / 顶面

比例 1:5 / 模型1:1 mm

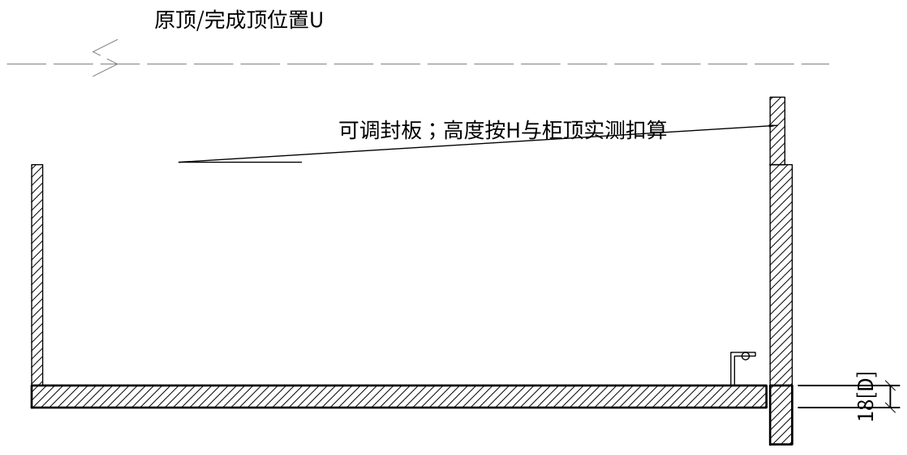


柜高2400为D；顶部剩余高度由实测H扣算。
上封板与顶面设置可调整的收边关系。
角码及螺钉只表达固定位置，规格和间距另核。
吊顶不得作为高柜唯一固定基层。
未核梁底及检修空间前，不确定封板下料高。

节点深化 / D03 · D04

所有未标P的节点尺寸与连接构造均为D；原基层及未确认条件标U

D03 门板分缝 / 侧板 / 五金


比例 1:2 / 模型1:1 mm

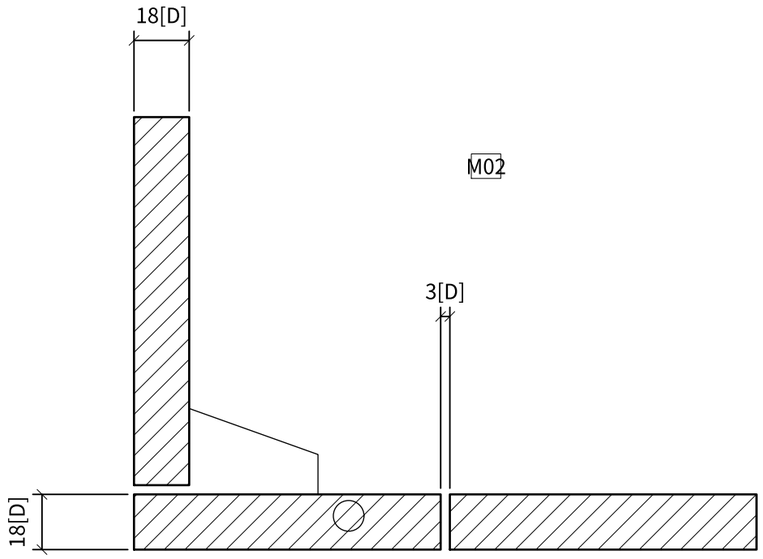

门板18、侧板18、门缝3均D。
覆门形式按示意；杯铰链、覆盖量与封边共同复核。
定位模数不等于门板净宽；不得用图面分格直接下料。
男孩房门套邻柜仅20[P]，侧封板及开启需协调。

D04 织物软饰面 / 基层 / 木边框

比例 1:2 / 模型1:1 mm

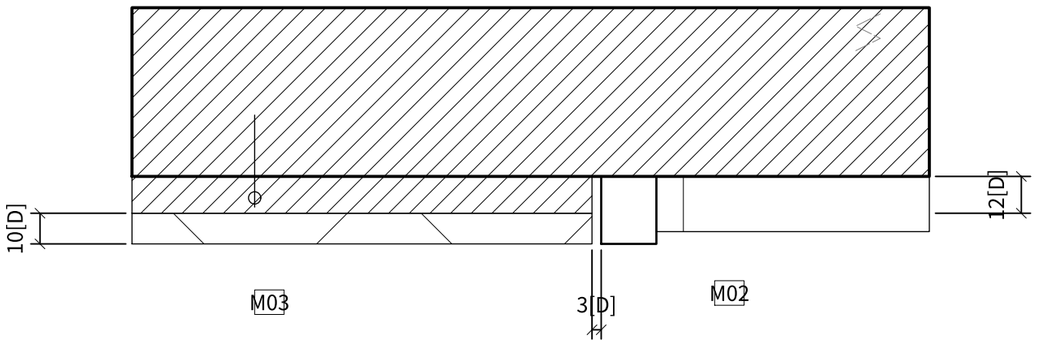


建议软饰层10+基层12[D]，沿墙铺设。
木边框与软饰面之间留3[D]控制缝。
基层固定到原墙可用基层，禁止只粘于松散面层。
固定及防火要求随样板、基层和产品体系确认。
效果图的织物与木边关系保留，材质样板仍待确认。

节点深化 / D05 · D06

所有未标P的节点尺寸与连接构造均为D；原基层及未确认条件标U

D05 原窗框 / 窗套 / 墙面收边


比例 1:2 / 模型1:1 mm

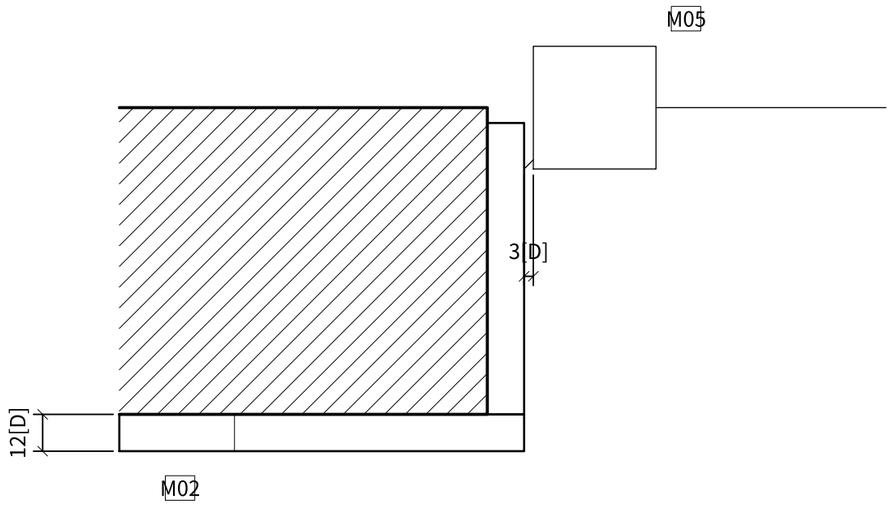

窗套基层及饰面合计12[D]；框边控制缝3[D]。
密封材料与原窗框兼容，保留排水及检修空间。
不以饰面压住原窗开启、压线或排水构件。
原墙厚、窗框截面及固定U，图示不替代原窗深化图。

D06 桌面 / 窗台 / 窗边座协调

比例 1:15 / 模型1:1 mm

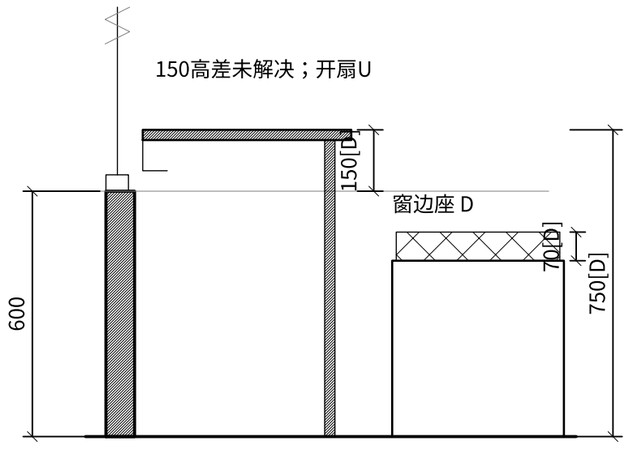


原标窗台600[P]；桌高750、板厚25均D。
桌面高于窗台150，图中明确表示该冲突。
窗边座高500[D]，其中坐垫70[D]。
桌板支承/角码固定到可靠基层，规格按跨距另核。
窗扇开启范围U；取得现场数据前不作为安装定案。

节点深化 / D07 · D08

所有未标P的节点尺寸与连接构造均为D；原基层及未确认条件标U

D07 窗帘槽 / 轨道 / 吊顶端部


比例 1:5 / 模型1:1 mm

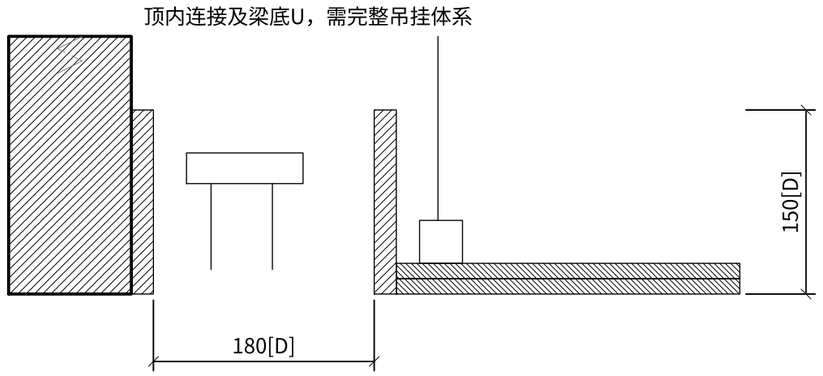

槽净宽180、建议预留深150均D。
顶面板12.5+12.5[D]，需完整龙骨与吊挂体系。
轨道/电机按产品实物复核，保留检修可达性。
原顶、梁底及H未确认；节点不确定房间吊顶标高。

D08 层板 / 明装灯带型材 / 走线

比例 1:2 / 模型1:1 mm

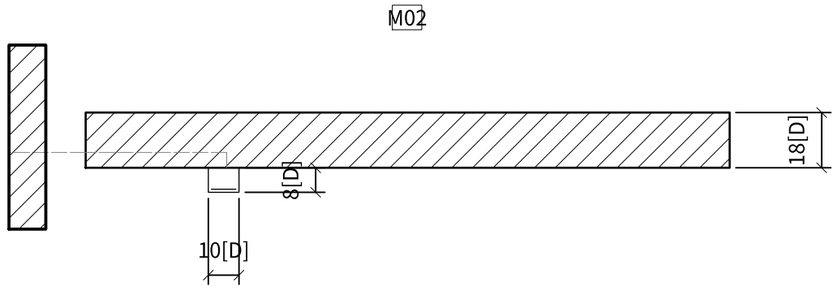


承载层板18[D]连续保留。
改为板底明装10×8[D]型材预留，不切掉10深承载截面。
型材需先选型，扩散罩及散热空间按厂家确认。
走线进入侧板背部；驱动置于可检修位置。
大跨层板的支承和荷载需单独复核。

节点深化 / D09

所有未标P的节点尺寸与连接构造均为D；原基层及未确认条件标U

D09 踢脚端头 / 门套 / 墙角

比例 1:5 / 模型1:1 mm

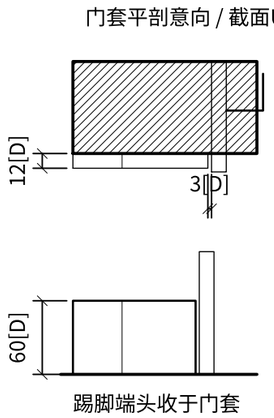

踢脚高60、厚12均D，端头收于门套边。
门套板12[D]、框边3[D]控制缝。
门扇厚与门框截面U，平剖仅表达收边关系。
地面与墙面完成厚度待核；门缝、开启及密封按成品门系统。

接口检查重点

柜体必须核对门扇、抽屉、窗扇和检修空间。
窗套、门套与踢脚应连续收口并区分原有与新增。
没有完整现场数据的接口保留U；文件审计通过不等于节点已具备施工条件。