西湖豪庭 2#2单元603｜图纸目录与材料图例

参照参考图的制图组织方式深化；本项目的尺寸、材料及构造独立标注

01 图纸目录 / 13张

GE-00	图纸目录、材料图例、尺寸状态
GE-01	原平面矢量索引与四向视线
EL-01 / 02	主卧 A/B、C/D 立面
EL-03 / 04	次卧 A/B、C/D 立面
EL-05 / 06	女儿房 A/B、C/D 立面
EL-07 / 08	男孩房 A/B、C/D 立面
ND-01 / 02	D01—D06建议节点详图
GE-02	设计建议尺寸表及协调事项

02 制图与尺寸状态

原图确认：平面总宽、柜体外轮廓、门扇跨度；不加[D]。


[D]设计建议：柜高、模块、门缝、台高、板厚、构造做法。

H主/H次/H女/H男为待确认完成净高；不套用参考项目2400/2800。

已有窗高1810及LD600按原标保留；完成地面基准需核实。


新增建议构造须经选材、现场复尺及厂家校核后才能下料。

03 材料图例（效果图意向；样板待确认）

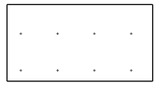


M01

暖白/浅米墙面涂装

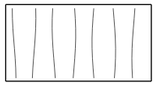


M02

自然木色饰面与木作

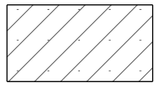

M03

米色织物/软饰面

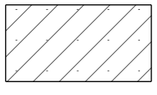


M04

儿童床粉/绿装饰面




M05

原窗黑框玻璃

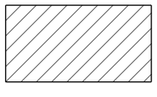


M07

顶面/窗帘槽意向

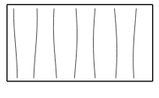

M06

木地板效果，规格待定

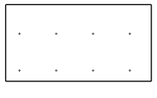

M08

蓝色装饰面意向

图纸状态：深化建议稿，不是完成签审的施工图。图纸只增加有标识的设计建议，不把拟定值冒充原图实测值。

单位mm；[D]均为拟定值。图形竖向不代替实测H；节点是建议做法，确认后方可进入施工签审。

XI HU

卧室深化

R03 / 2026.10.16

项目

西湖豪庭603

范围

图纸目录与材料图例

图号

GE-00

比例

索引/说明不按比例

竖向

参数/建议尺寸

状态

深化建议稿

制图

CAD矢量绘制

核对

源图/效果方案

审核

待设计审核

签认

待业主确认

尺寸状态

无[D]：原图/几何

[D]：设计建议

H：完成净高待核

门扇宽≠洞口净宽

材质样板待确认

不作直接下料依据

参考表达：

黑白线宽/分格

多级尺寸/材料


未完成施工签审

西湖豪庭 2#2单元603｜原平面索引 / A B C D

索引示意；数字及轮廓依据原DXF。门扇宽与门洞净宽分别核对。

E-01 主卧


基准宽5200；展开深3790（有错台，以轮廓为准）

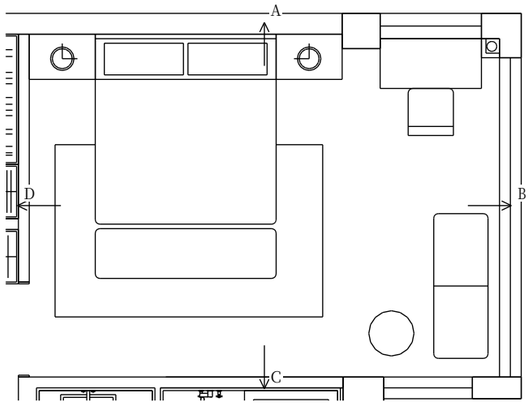

源平面矢量描取；门扇宽不等待核。|净宽；柜体高度仍

E-02 次卧（效果图称老人房）


基准宽3420；展开深3430（有错台，以轮廓为准）

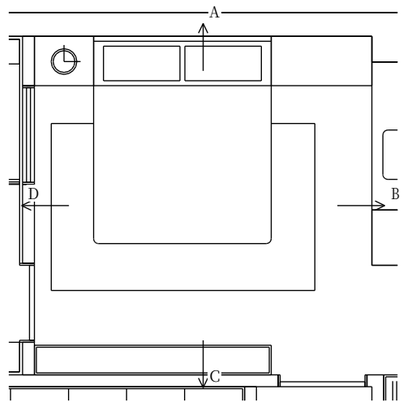

源平面矢量描取；门扇宽不等待核。|净宽；柜体高度仍

E-03 女儿房


基准宽5450；展开深3010（有错台，以轮廓为准）

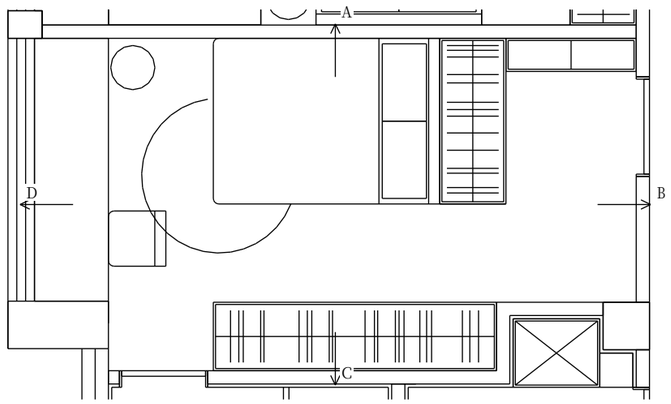

源平面矢量描取；门扇宽不等待核。|净宽；柜体高度仍

E-04 男孩房

基准宽5450；展开深2870（有错台，以轮廓为准）

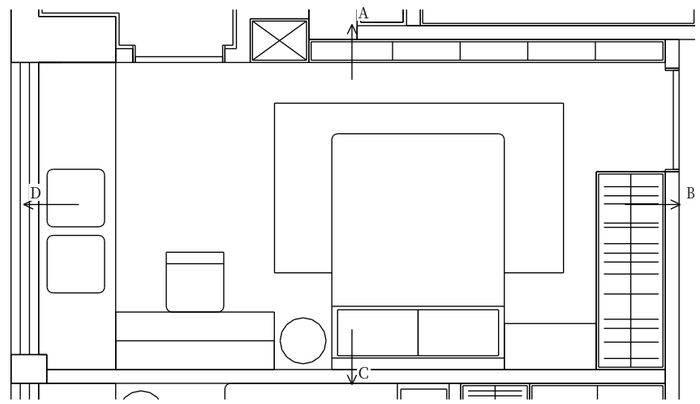

北柜深200；柜前2670、柜内链2690、柜后墙2870，基准不同。

北侧柜前2670、柜内链2690、柜后墙2870属于不同展开基准。西湖豪庭原图对象编号及坐标另附JSON。

单位mm；[D]均为拟定值。图形竖向不代替实测H；节点是建议做法，确认后方可进入施工签审。

XI HU

卧室深化

R03 / 2026.10.16

项目

西湖豪庭603

范围

原平面索引 / A B C

图号

GE-01

比例

索引/说明不按比例

竖向

参数/建议尺寸

状态

深化建议稿

制图

CAD矢量绘制

核对

源图/效果方案

审核

待设计审核

签认

待业主确认

尺寸状态

无[D]：原图/几何

[D]：设计建议

H：完成净高待核

门扇宽≠洞口净宽

材质样板待确认

不作直接下料依据

参考表达：

黑白线宽/分格


多级尺寸/材料

未完成施工签审

西湖豪庭 2#2单元603｜主卧立面 A/B


立面深化建议 · 以西湖豪庭原图为平面依据；未知总高不套用参考项目
平面5200×3790；深3790由墙线几何读取。床2000×2100。衣帽间另区不展开。

01A 朝原平面图上侧｜主卧

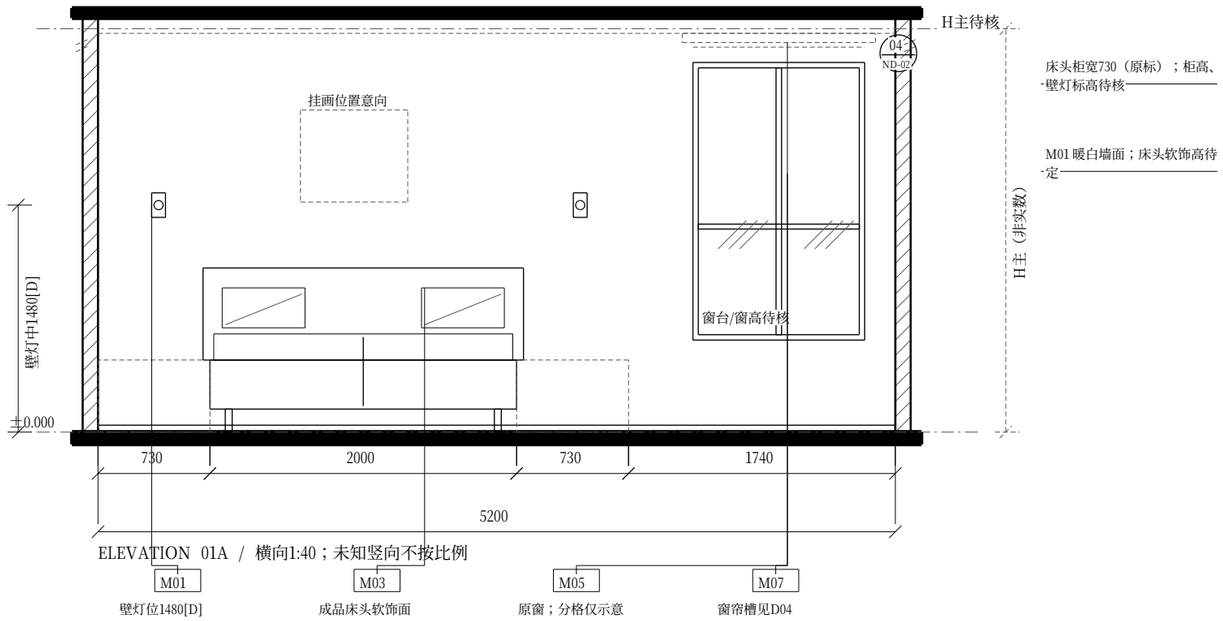

ELEVATION 01A / 横向1:40；未知竖向不按比例

01B 朝原平面图右侧｜主卧

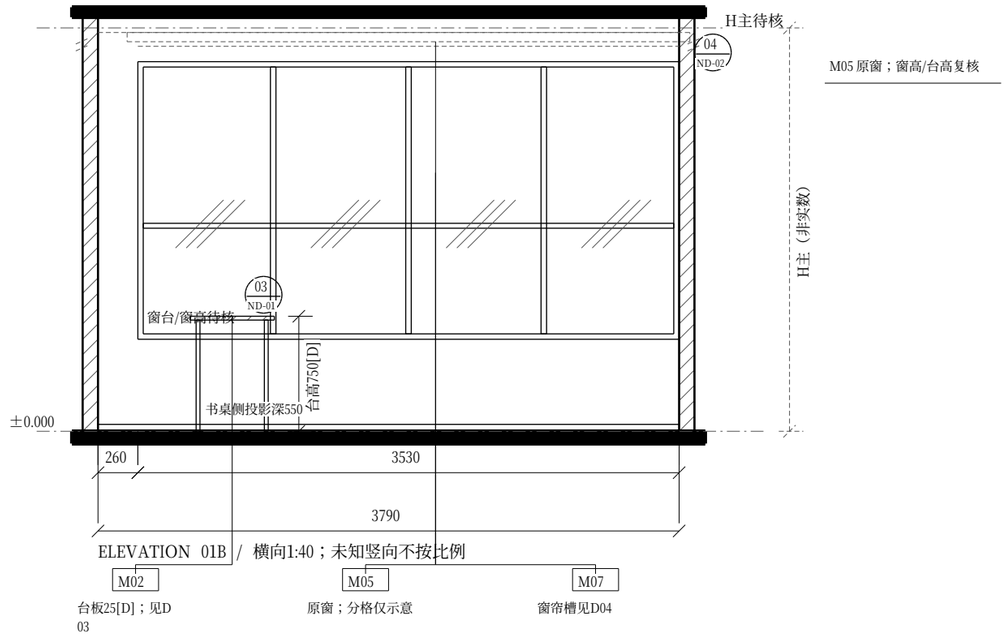

ELEVATION 01B / 横向1:40；未知竖向不按比例

单位mm；[D]均为拟定值。图形竖向不代替实测H；节点是建议做法，确认后方可进入施工签审。

XI HU

卧室深化

R03 / 2026.10.16

项目
西湖豪庭603

范围
主卧立面 A/B

图号
EL-01

比例
横向1:40

竖向
参数/建议尺寸

状态
深化建议稿

制图
CAD矢量绘制

核对
源图/效果方案

审核
待设计审核

签认
待业主确认

尺寸状态

无[D]：原图/几何

[D]：设计建议

H：完成净高待核

门扇宽≠洞口净宽

材质样板待确认

不作直接下料依据

参考表达：

黑白线宽/分格


多级尺寸/材料

未完成施工签审

西湖豪庭 2#2单元603｜主卧立面 C/D


立面深化建议 · 以西湖豪庭原图为平面依据；未知总高不套用参考项目
平面5200×3790；深3790由墙线几何读取。床2000×2100。衣帽间另区不展开。

01C 朝原平面图下侧｜主卧

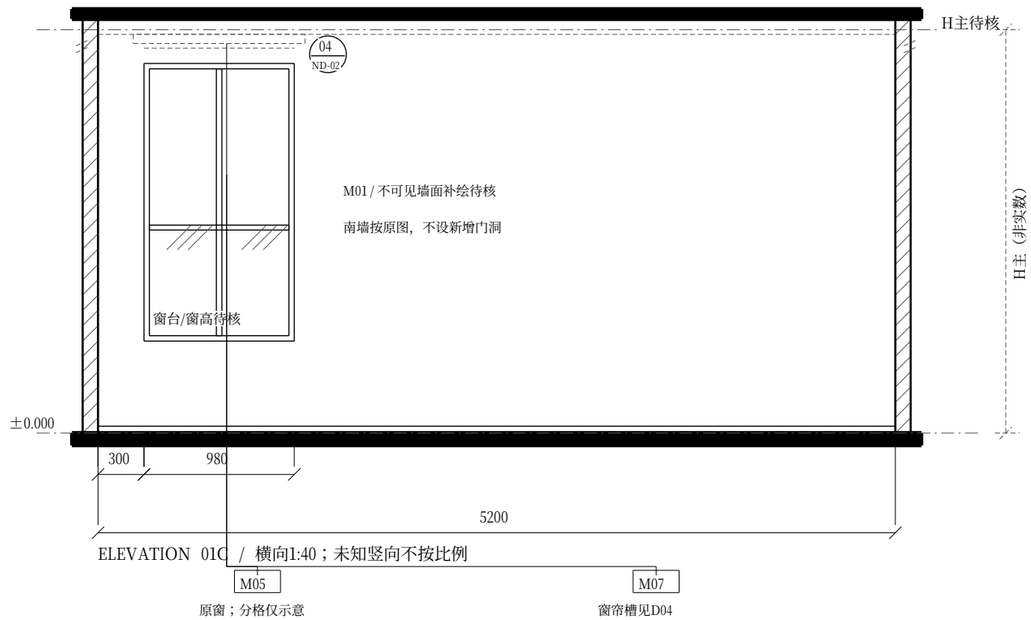

ELEVATION 01C / 横向1:40；未知竖向不按比例

01D 朝原平面图左侧｜主卧

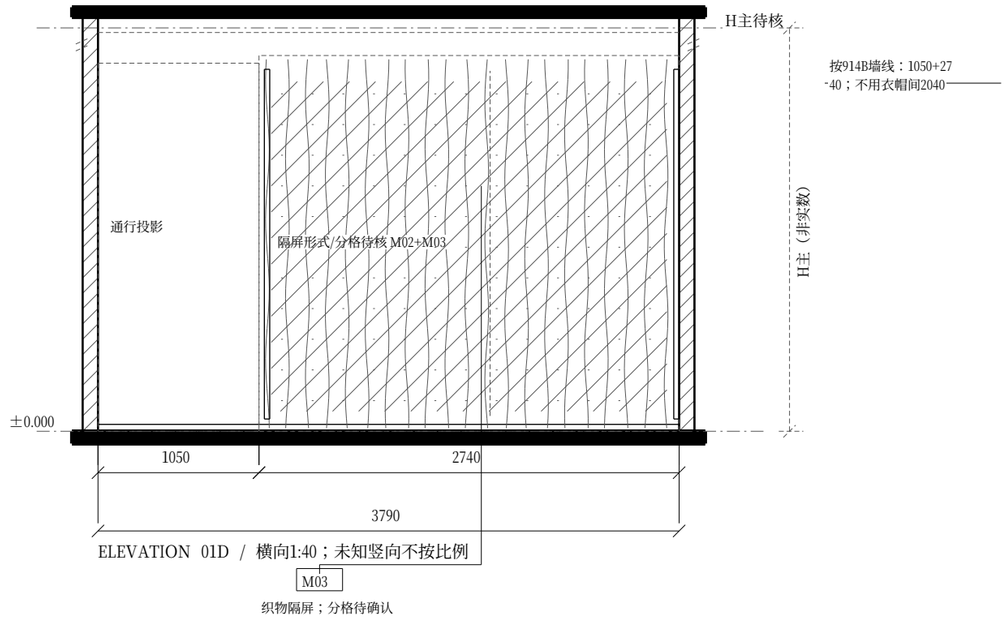

ELEVATION 01D / 横向1:40；未知竖向不按比例

单位mm；[D]均为拟定值。图形竖向不代替实测H；节点是建议做法，确认后方可进入施工签审。

XI HU

卧室深化

R03 / 2026.10.16

项目
西湖豪庭603

范围
主卧立面 C/D

图号
EL-02

比例
横向1:40

竖向
参数/建议尺寸

状态
深化建议稿

制图
CAD矢量绘制

核对
源图/效果方案

审核
待设计审核

签认
待业主确认

尺寸状态

无[D]：原图/几何

[D]：设计建议

H：完成净高待核

门扇宽≠洞口净宽

材质样板待确认

不作直接下料依据

参考表达：

黑白线宽/分格

多级尺寸/材料


未完成施工签审

西湖豪庭 2#2单元603｜次卧（效果图称老人房）立面 A/B

立面深化建议 · 以西湖豪庭原图为平面依据；未知总高不套用参考项目


3420=600+1800+1020；3430=2100+1030+300。床1800×2100。

02A 朝原平面图上侧｜次卧（效果图称老人房）

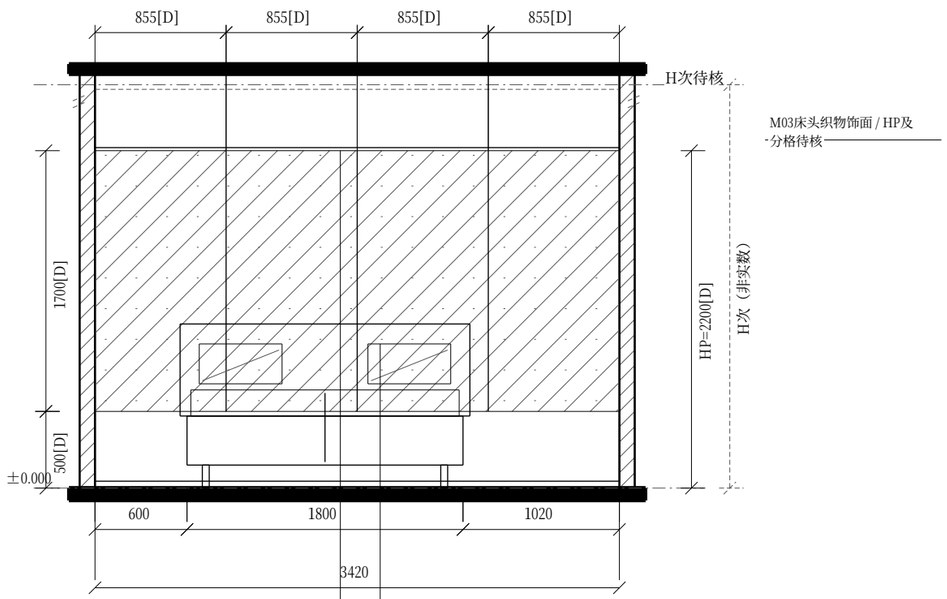

ELEVATION 02A / 横向1:40；未知竖向不按比例

02B 朝原平面图右侧｜次卧（效果图称老人房）

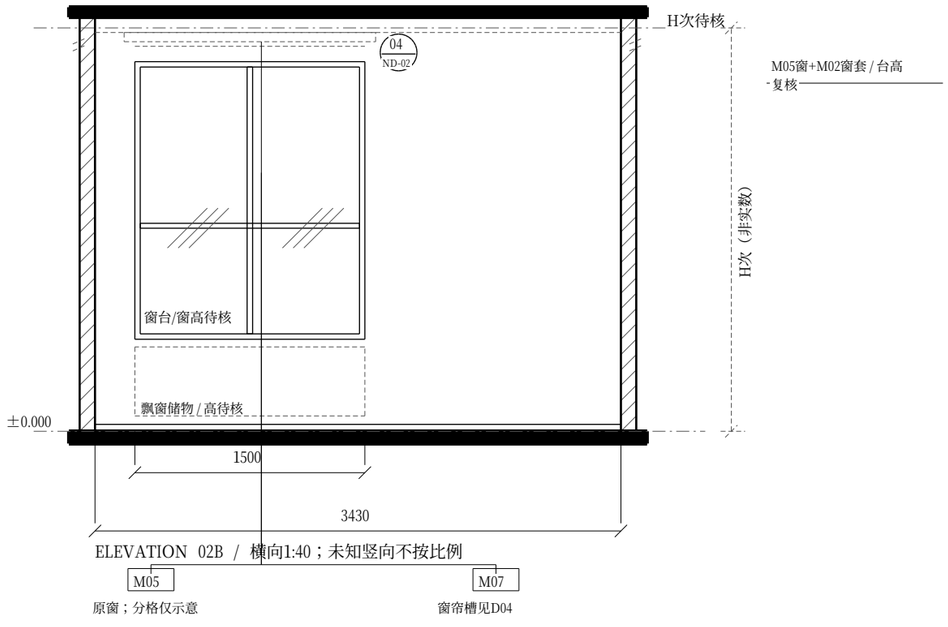

ELEVATION 02B / 横向1:40；未知竖向不按比例

单位mm；[D]均为拟定值。图形竖向不代替实测H；节点是建议做法，确认后方可进入施工签审。

XI HU

卧室深化

R03 / 2026.10.16

项目
西湖豪庭603

范围
次卧（效果图称老人房）立面

图号
EL-03

比例
横向1:40

竖向
参数/建议尺寸

状态
深化建议稿

制图
CAD矢量绘制

核对
源图/效果方案

审核
待设计审核

签认
待业主确认

尺寸状态

无[D]：原图/几何

[D]：设计建议

H：完成净高待核

门扇宽≠洞口净宽

材质样板待确认

不作直接下料依据

参考表达：

黑白线宽/分格

多级尺寸/材料


未完成施工签审

西湖豪庭 2#2单元603｜次卧（效果图称老人房）立面 C/D

立面深化建议 · 以西湖豪庭原图为平面依据；未知总高不套用参考项目


3420=600+1800+1020；3430=2100+1030+300。床1800×2100。

02C 朝原平面图下侧｜次卧（效果图称老人房）

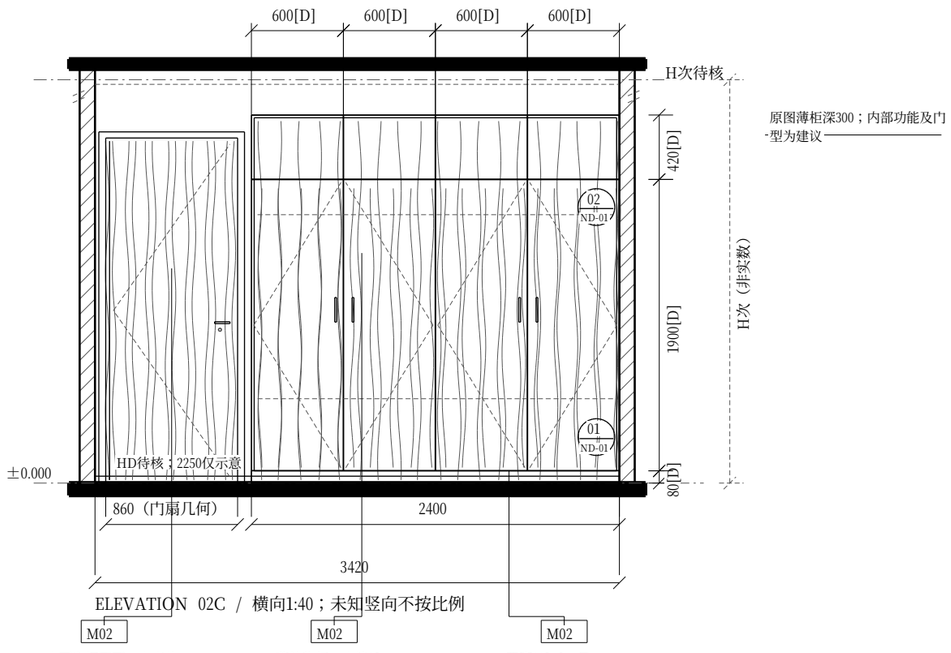

ELEVATION 02C / 横向1:40；未知竖向不按比例

02D 朝原平面图左侧｜次卧（效果图称老人房）

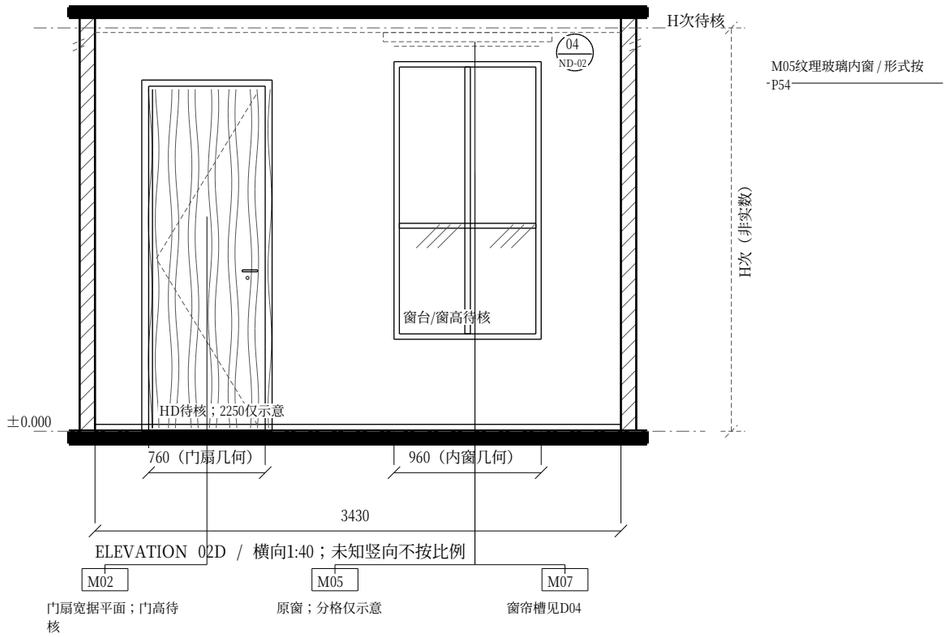

ELEVATION 02D / 横向1:40；未知竖向不按比例

单位mm；[D]均为拟定值。图形竖向不代替实测H；节点是建议做法，确认后方可进入施工签审。

XI HU

卧室深化

R03 / 2026.10.16

项目
西湖豪庭603

范围
次卧（效果图称老人房）立面

图号
EL-04

比例
横向1:40

竖向
参数/建议尺寸

状态
深化建议稿

制图
CAD矢量绘制

核对
源图/效果方案

审核
待设计审核

签认
待业主确认

尺寸状态

无[D]：原图/几何

[D]：设计建议

H：完成净高待核

门扇宽≠洞口净宽

材质样板待确认

不作直接下料依据

参考表达：

黑白线宽/分格

多级尺寸/材料


未完成施工签审

西湖豪庭 2#2单元603｜女儿房立面 A/B

立面深化建议 · 以西湖豪庭原图为平面依据；未知总高不套用参考项目

5450=670+950+2050+600+1180；3010=1500+890+620。床1500×2050。


03A 朝原平面图上侧｜女儿房

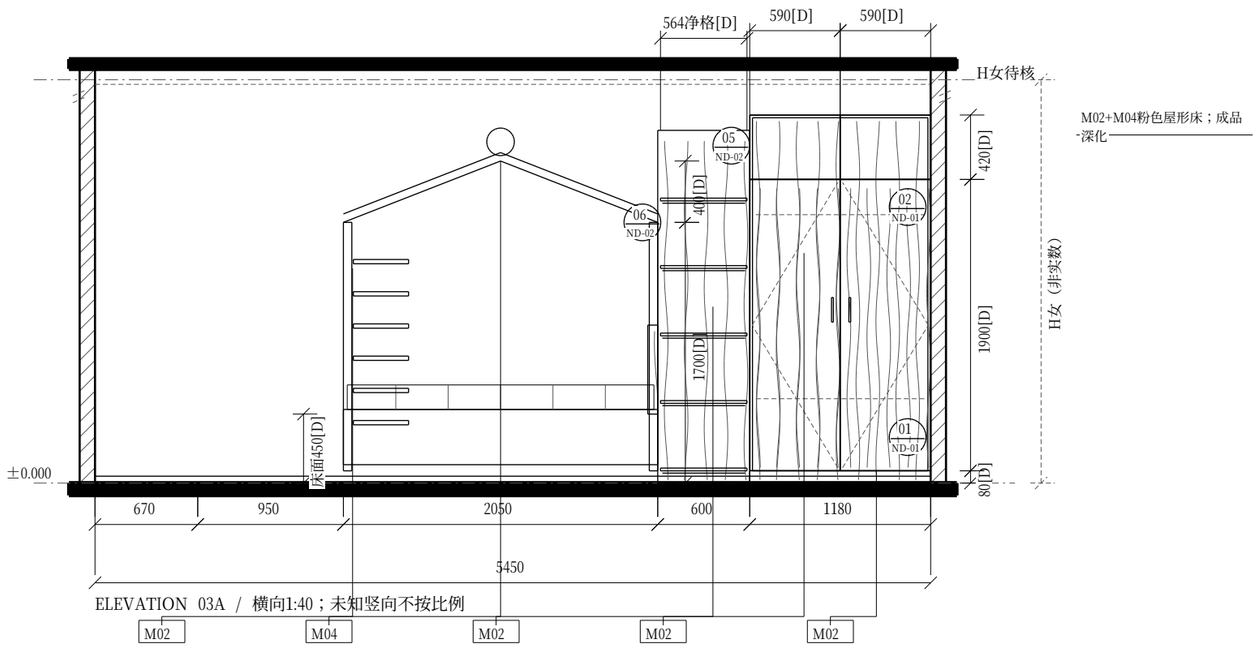

ELEVATION 03A / 横向1:40；未知竖向不按比例

M02	M04	M02	M02	M02
成品床造型见D06	粉/绿色装饰面意向	层板18[D]；灯槽 D05	杂物柜；门缝3[D]	踢脚80[D]；见D 01

03B 朝原平面图右侧｜女儿房

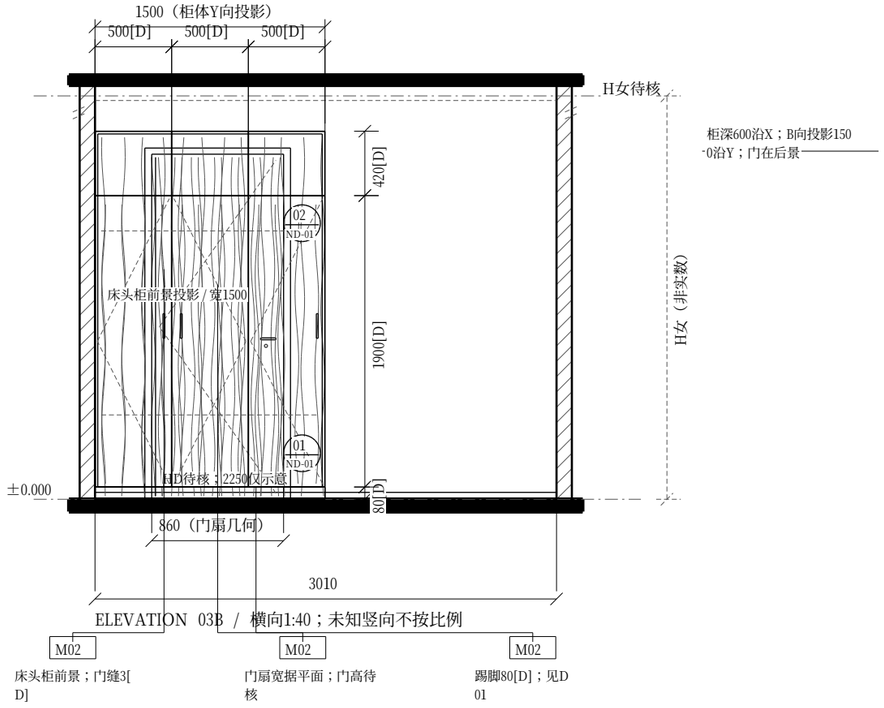

ELEVATION 03B / 横向1:40；未知竖向不按比例

M02	M02	M02
床头柜前景；门缝3[D]	门扇宽据平面；门高待核	踢脚80[D]；见D 01

单位mm；[D]均为拟定值。图形竖向不代替实测H；节点是建议做法，确认后方可进入施工签审。

XI HU

卧室深化

R03 / 2026.10.16

项目
西湖豪庭603

范围
女儿房立面 A/B

图号
EL-05

比例
横向1:40

竖向
参数/建议尺寸

状态
深化建议稿

制图
CAD矢量绘制

核对
源图/效果方案

审核
待设计审核

签认
待业主确认

尺寸状态

无[D]：原图/几何

[D]：设计建议

H：完成净高待核

门扇宽≠洞口净宽

材质样板待确认

不作直接下料依据

参考表达：

黑白线宽/分格

多级尺寸/材料


未完成施工签审

西湖豪庭 2#2单元603｜女儿房立面 C/D

立面深化建议 · 以西湖豪庭原图为平面依据；未知总高不套用参考项目

5450=670+950+2050+600+1180；3010=1500+890+620。床1500×2050。


03C 朝原平面图下侧｜女儿房

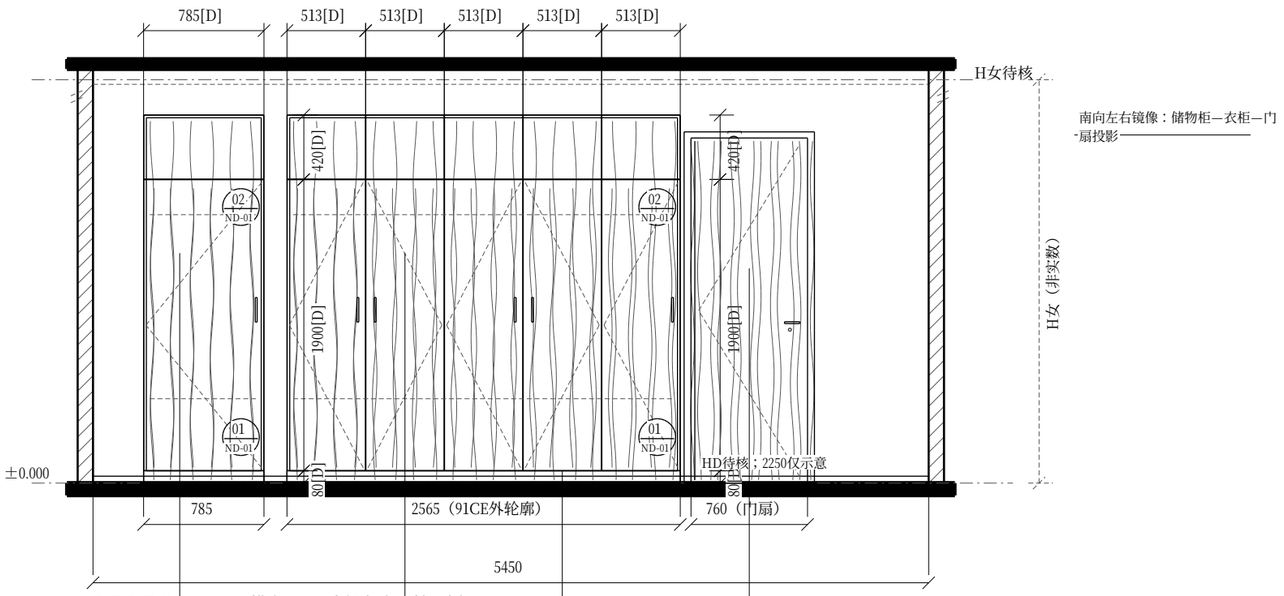

ELEVATION 03C / 横向1:40；未知竖向不按比例

M02	M02	M02	M02
储物柜；门缝3[D]	衣柜；门缝3[D]	踢脚80[D]；见D01	门扇宽据平面；门高待核

03D 朝原平面图左侧｜女儿房

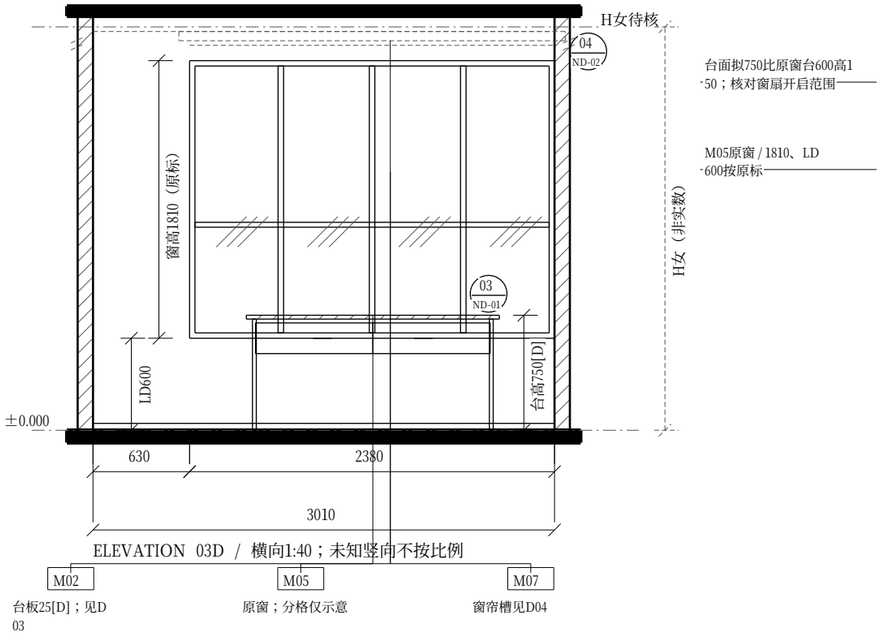

ELEVATION 03D / 横向1:40；未知竖向不按比例

M02	M05	M07
台板25[D]；见D03	原窗；分格仅示意	窗帘槽见D04

单位mm；[D]均为拟定值。图形竖向不代替实测H；节点是建议做法，确认后方可进入施工签审。

XI HU

卧室深化

R03 / 2026.10.16

项目
西湖豪庭603

范围
女儿房立面 C/D

图号
EL-06

比例
横向1:40

竖向
参数/建议尺寸

状态
深化建议稿

制图
CAD矢量绘制

核对
源图/效果方案

审核
待设计审核

签认
待业主确认

尺寸状态

无[D]：原图/几何

[D]：设计建议

H：完成净高待核

门扇宽≠洞口净宽

材质样板待确认

不作直接下料依据

参考表达：

黑白线宽/分格


多级尺寸/材料

未完成施工签审

西湖豪庭 2#2单元603｜男孩房立面 A/B


立面深化建议 · 以西湖豪庭原图为平面依据；未知总高不套用参考项目
北侧柜后墙基准深2870（几何）；2690链至柜内线，不作净深。床1500×2050。

04A 朝原平面图上侧｜男孩房

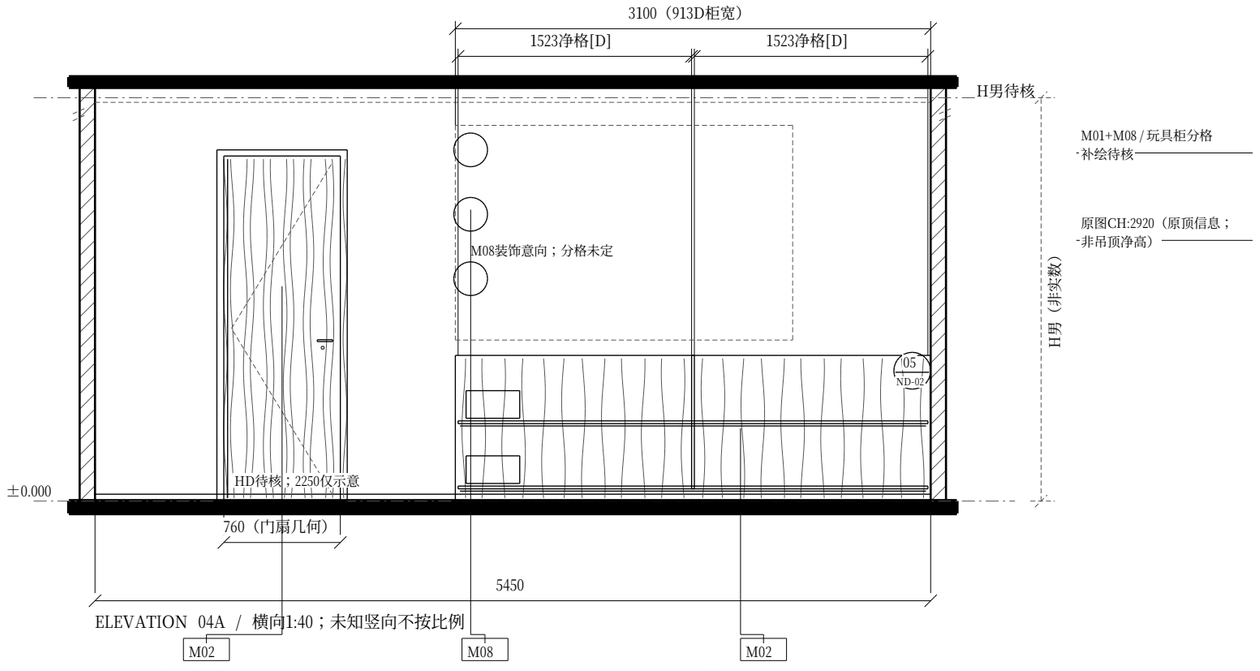

ELEVATION 04A / 横向1:40；未知竖向不按比例

04B 朝原平面图右侧｜男孩房

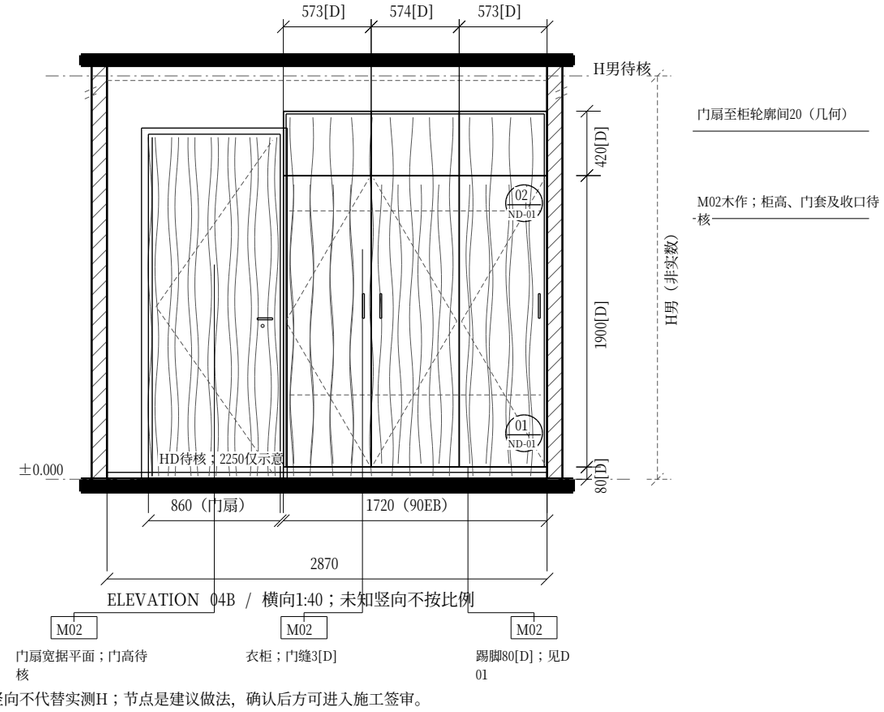

ELEVATION 04B / 横向1:40；未知竖向不按比例

单位mm；[D]均为拟定值。图形竖向不代替实测H；节点是建议做法，确认后方可进入施工签审。

XIHU

卧室深化

R03 / 2026.10.16

项目
西湖豪庭603

范围
男孩房立面 A/B

图号
EL-07

比例
横向1:40

竖向
参数/建议尺寸

状态
深化建议稿

制图
CAD矢量绘制

核对
源图/效果方案

审核
待设计审核

签认
待业主确认

尺寸状态

无[D]：原图/几何

[D]：设计建议

H：完成净高待核

门扇宽≠洞口净宽

材质样板待确认

不作直接下料依据

参考表达：

黑白线宽/分格


多级尺寸/材料

未完成施工签审

西湖豪庭 2#2单元603｜男孩房立面 C/D


立面深化建议 · 以西湖豪庭原图为平面依据；未知总高不套用参考项目
北侧柜后墙基准深2870（几何）；2690链至柜内线，不作净深。床1500×2050。

04C 朝原平面图下侧｜男孩房

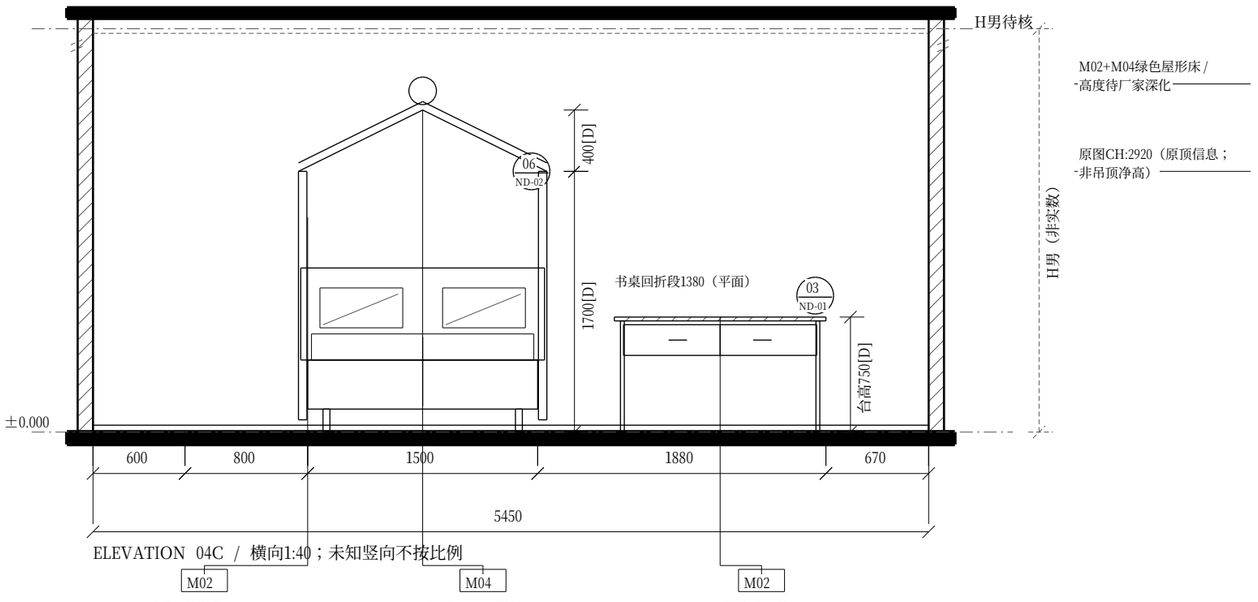

ELEVATION 04C / 横向1:40；未知竖向不按比例

04D 朝原平面图左侧｜男孩房

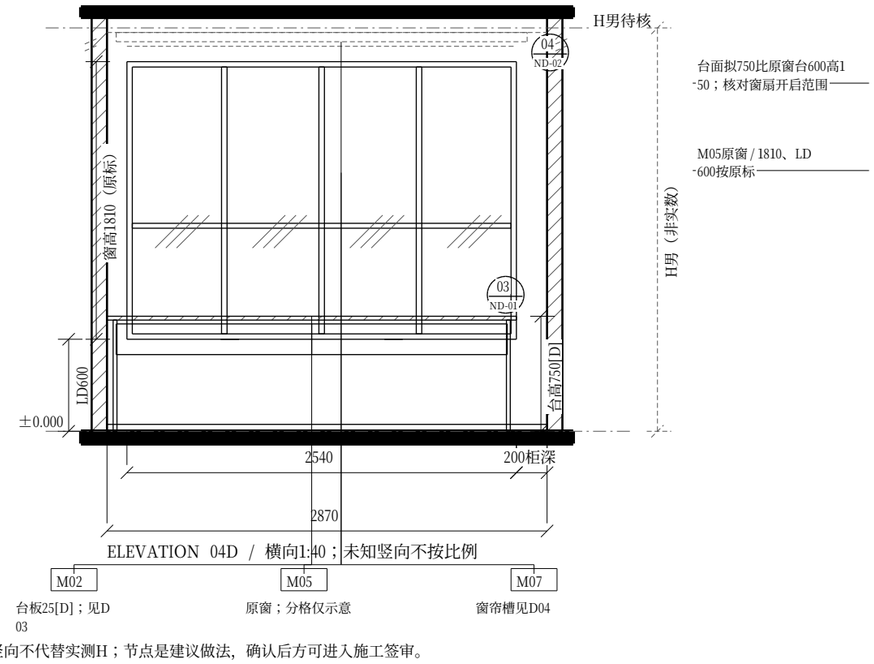

ELEVATION 04D / 横向1:40；未知竖向不按比例

单位mm；[D]均为拟定值。图形竖向不代替实测H；节点是建议做法，确认后方可进入施工签审。

XI HU

卧室深化

R03 / 2026.10.16

项目
西湖豪庭603

范围
男孩房立面 C/D

图号
EL-08

比例
横向1:40

竖向
参数/建议尺寸

状态
深化建议稿

制图
CAD矢量绘制

核对
源图/效果方案

审核
待设计审核

签认
待业主确认

尺寸状态

无[D]：原图/几何

[D]：设计建议

H：完成净高待核

门扇宽≠洞口净宽

材质样板待确认

不作直接下料依据

参考表达：

黑白线宽/分格


多级尺寸/材料

未完成施工签审

西湖豪庭 2#2单元603｜建议节点 D01—D03

以下全部尺寸为[D]设计建议。节点放大示意；原墙、固定件和材料选型需确认。

01 柜体踢脚与板件构成 / 1:5

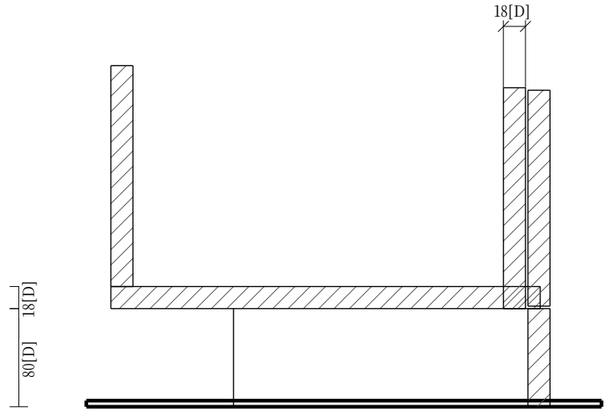


柜底板/侧板18[D]；门板18[D]

踢脚80[D]；可调脚规格按柜厂

饰面M02；收口与地坪标高复核

D01用于立面中的柜体底部；板厚、踢脚及调节构件均属建议，非已确认下料规格。

02 覆门与分缝平剖示意 / 1:2

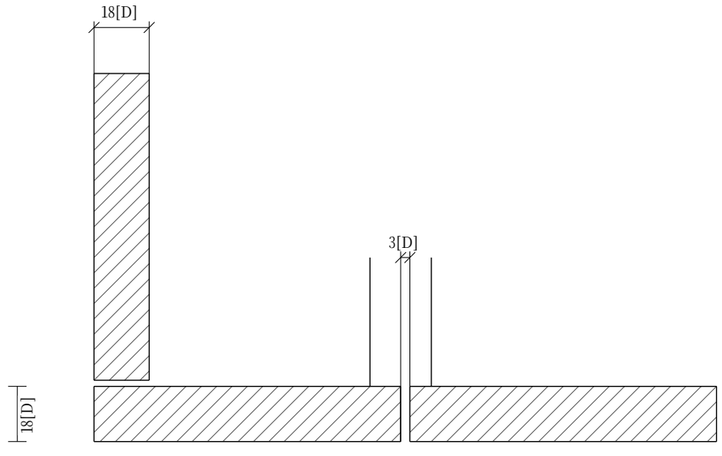


门缝3[D]；以模块定位，不直接作门板下料

铰链及覆盖量应与厂家五金共同校核

立面虚线V为建议开启方式；不是玻璃纹理

03 桌板边口 / 台高协调 / 1:2

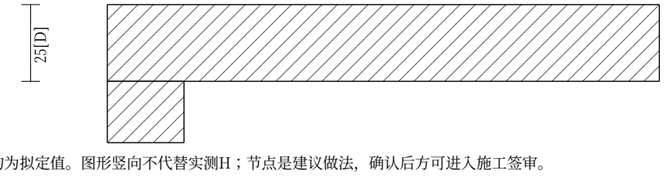

拟台高750[D]；原窗台600 → 台面高出150

须确认下固定扇/开扇范围；未确认前不下单

台面支承连接由柜厂结合跨度与基层深化

单位mm；[D]均为拟定值。图形竖向不代替实测H；节点是建议做法，确认后方可进入施工签审。

XI HU

卧室深化

R03 / 2026.10.16

项目
西湖豪庭603

范围
建议节点 D01—D03

图号
ND-01

比例
详见各节点

竖向
参数/建议尺寸

状态
深化建议稿

制图
CAD矢量绘制

核对
源图/效果方案

审核
待设计审核

签认
待业主确认

尺寸状态

无[D]：原图/几何

[D]：设计建议

H：完成净高待核

门扇宽≠洞口净宽

材质样板待确认

不作直接下料依据

参考表达：

黑白线宽/分格


多级尺寸/材料

未完成施工签审

西湖豪庭 2#2单元603｜建议节点 D04—D06

节点为可审阅的构造建议；构造材料、连接及设备尺寸需专项复核。

04 窗帘槽与顶面关系 / 1:5

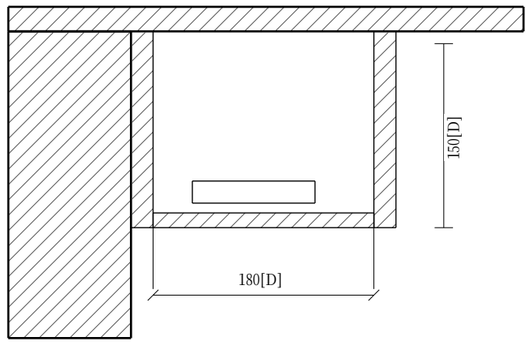


槽净宽180[D]、预留深150[D]

轨道、电机及检修净距按选型复核

H与梁底未核；不以节点示意确定吊顶标高

05 层板灯槽与走线 / 1:2

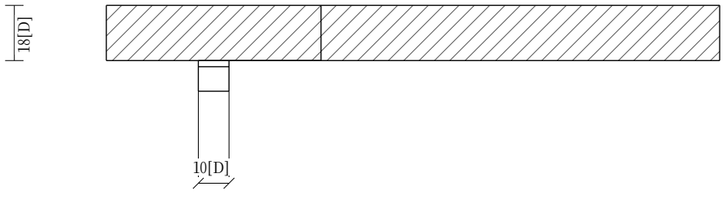


层板18[D]；示意槽10×10[D]

按铝型材实物复核开槽，不以示意代替选型

灯带驱动位置需可检修；线路位置另协调

06 儿童床屋形造型控制 / 不按结构比例

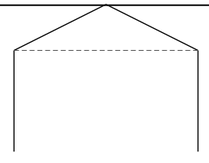

柱高1700[D]、屋顶起坡400[D]仅为造型建议

成品床框架、攀爬架、连接与承载由厂家设计

需取得实物尺寸及安装图；本节点不是受力节点

单位mm；[D]均为拟定值。图形竖向不代替实测H；节点是建议做法，确认后方可进入施工签审。

XI HU

卧室深化

R03 / 2026.10.16

项目
西湖豪庭603

范围
建议节点 D04—D06

图号
ND-02

比例
详见各节点

竖向
参数/建议尺寸

状态
深化建议稿

制图
CAD矢量绘制

核对
源图/效果方案

审核
待设计审核

签认
待业主确认

尺寸状态

无[D]：原图/几何

[D]：设计建议

H：完成净高待核

门扇宽≠洞口净宽

材质样板待确认

不作直接下料依据

参考表达：

黑白线宽/分格

多级尺寸/材料

未完成施工签审

西湖豪庭 2#2单元603｜建议尺寸表 / 待核协调

数字更多必须对应明确的设计状态；以下建议尚未获得现场或选型确认。

01 原图与建议的边界

柜高	2400[D]	设计建议；条件H需大于柜体及顶部收口要求
柜体板件/门板	18[D]	按实际板材、门板覆盖量、封边与五金校核
柜门缝	3[D]	模块尺寸不直接等于门板下料宽
柜踢脚	80[D]	与地面完成面、调节脚及底板构造共同确认
书桌台高/台厚	750 / 25[D]	原窗台600；高差150，需确认原窗开扇范围
柜层板	18[D]	跨度与支承方式交柜厂复核，不暗示承载能力
窗帘槽净宽/深	180 / 150[D]	窗帘轨道、电机和检修距离按实物
儿童床屋形	1700+400[D]	仅造型建议；不替代成品厂家安装及结构图
次卧软饰面上口	2200[D]	拟分格855×4；基层、面层及灯槽做法待确认

02 当前仍待确认

四间完成地面至吊顶净高H，以及梁底/原顶/地坪完成厚度的关系。

门洞净高与门扇尺寸、移门轨道、门套和柜体之间的收口。

原窗保留条件、窗台基准、开扇范围以及窗边书桌台面协调。

壁灯建议中高1480[D]、开关插座与家具的最终定位；不替代机电图。

材料品牌、色号、基层、板厚和样板，以及节点连接的现场适用性。

儿童床厂商图纸与固定条件；图中屋形并非结构设计。

03 相比R02的实际新增

16个立面全部改为两幅/页；黑白线宽、材料纹理、开启V线、柜体内线及多级尺寸。

以西湖豪庭修订后的原始轮廓为基础增加可标识的柜门模数、门缝、层板和台面构成。

D01—D06均有实际节点图，与立面索引对应；不是只有索引编号。

参考PDF仅用于制图深度研究；未复制其项目数据、公司图标、签字或整页图面。

单位mm；[D]均为拟定值。图形竖向不代替实测H；节点是建议做法，确认后方可进入施工签审。

XI HU

卧室深化

R03 / 2026.10.16

项目
西湖豪庭603

范围
建议尺寸表 / 待核协调

图号
GE-02

比例
索引/说明不按比例

竖向
参数/建议尺寸

状态
深化建议稿

制图
CAD矢量绘制

核对
源图/效果方案

审核
待设计审核

签认
待业主确认

尺寸状态

无[D]：原图/几何

[D]：设计建议

H：完成净高待核

门扇宽≠洞口净宽

材质样板待确认

不作直接下料依据

参考表达：

黑白线宽/分格

多级尺寸/材料

未完成施工签审